

ATLANTIC BEACH COUNTRY CLUB UNIT 2

Being a replat of all of Lot 5 of Donner's Replat and a portion Section 8 and Section 17, Township 2 South, Range 29 East, the City of Jacksonville, and the City of Atlantic Beach, Duval County, Florida

CAPTION

THAT CERTAIN TRACT OR PARCEL OF LAND BEING ALL OF LOT 5 OF DONNER'S REPLAT, ACCORDING TO THE PLAT THEREOF AS RECORDED IN PLAT BOOK 19, PAGES 16 AND 16A OF THE PUBLIC RECORDS OF DUVAL COUNTY, FLORIDA AND A PORTION OF SECTION 8 AND SECTION 17, TOWNSHIP 2 SOUTH, RANGE 29 EAST, DUVAL COUNTY, FLORIDA, BEING MORE PARTICULARLY DESCRIBED AS FOLLOWS:

COMMENCING AT THE NORTHEAST CORNER OF LOT 1, BLOCK 9, SELVA MARINA UNIT NO. 5, ACCORDING TO THE PLAT THEREOF AS RECORDED IN PLAT BOOK 30, PAGE 29 OF THE CURRENT PUBLIC RECORDS OF DUVAL COUNTY, FLORIDA; THENCE SOUTH 12°16'40" EAST ALONG THE EASTERLY LINE OF SAID LOT 1 AND ITS SOUTHERLY EXTENSION THEREOF, SAID LINE ALSO BEING THE WESTERLY RIGHT-OF-WAY LINE OF SELVA MARINA DRIVE (A 100 FOOT RIGHT-OF-WAY), A DISTANCE OF 885.26 FEET TO A POINT ON A CURVE CONCAVE SOUTHWESTERLY; THENCE NORTHWESTERLY ALONG THE ARC OF SAID CURVE, HAVING A RADIUS OF 25.00 FEET AND A CENTRAL ANGLE OF 89°58'26", 39.26 FEET AND BEING SUBTENDED BY A CHORD BEARING AND DISTANCE OF NORTH 57°15'53" WEST, 35.35 FEET TO A POINT OF TANGENCY; THENCE SOUTH 77°44'55" WEST, 92.32 FEET TO A POINT OF CURVATURE OF A CURVE CONCAVE NORTHERLY; THENCE WESTERLY ALONG THE ARC OF SAID CURVE, HAVING A RADIUS OF 37.00 FEET AND A CENTRAL ANGLE OF 47°40'31", 312.03 FEET AND BEING SUBTENDED BY A CHORD BEARING AND DISTANCE OF NORTH 78°24'49" WEST, 303.11 FEET TO A POINT OF REVERSE CURVATURE OF A CURVE CONCAVE SOUTHWESTERLY; THENCE NORTHWESTERLY ALONG THE ARC OF SAID CURVE, HAVING A RADIUS OF 105.00 FEET AND A CENTRAL ANGLE OF 46°11'28", 84.65 FEET AND BEING SUBTENDED BY A CHORD BEARING AND DISTANCE OF NORTH 77°40'18" WEST, 82.38 FEET TO A POINT OF TANGENCY; THENCE SOUTH 79°13'58" WEST, 80.78 FEET TO A POINT OF CURVATURE OF A CURVE CONCAVE SOUTHEASTERLY; THENCE SOUTHWESTERLY ALONG THE ARC OF SAID CURVE, HAVING A RADIUS OF 135.00 FEET AND A CENTRAL ANGLE OF 13°09'05", 30.99 FEET AND BEING SUBTENDED BY A CHORD BEARING AND DISTANCE OF SOUTH 72°39'25" WEST, 30.92 FEET TO A POINT OF REVERSE CURVATURE OF A CURVE CONCAVE NORTHERLY; THENCE WESTERLY ALONG THE ARC OF SAID CURVE, HAVING A RADIUS OF 500.00 FEET AND A CENTRAL ANGLE OF 34°44'38", 181.92 FEET AND BEING SUBTENDED BY A CHORD BEARING AND DISTANCE OF SOUTH 83°27'12" WEST, 179.14 FEET TO A POINT OF COMPOUND CURVATURE OF A CURVE CONCAVE NORTHEASTERLY; THENCE NORTHWESTERLY ALONG THE ARC OF SAID CURVE, HAVING A RADIUS OF 400.00 FEET AND A CENTRAL ANGLE OF 36°53'28", 257.55 FEET AND BEING SUBTENDED BY A CHORD BEARING AND DISTANCE OF NORTH 60°43'46" WEST, 253.12 FEET TO A POINT OF TANGENCY; THENCE NORTH 42°17'02" WEST, 222.87 FEET; THENCE SOUTH 41°20'48" WEST, 80.00 FEET; THENCE SOUTH 80°05'47" WEST, 39.51 FEET; THENCE NORTH 56°23'49" WEST, 44.74 FEET; THENCE NORTH 73°00'05" WEST, 67.99 FEET TO THE POINT OF BEGINNING; THENCE SOUTH 73°01'49" WEST, 84.08 FEET; THENCE NORTH 80°24'17" WEST, 225.00 FEET; THENCE NORTH 65°08'58" WEST, 57.01 FEET; THENCE NORTH 75°39'28" WEST, 60.21 FEET; THENCE NORTH 80°24'17" WEST, 57.30 FEET; THENCE NORTH 89°27'38" WEST, 126.00 FEET TO A POINT ON A CURVE CONCAVE WESTERLY; THENCE SOUTHERLY ALONG THE ARC OF SAID CURVE, HAVING A RADIUS OF 200.00 FEET AND A CENTRAL ANGLE OF 4°52'22", 17.01 FEET AND BEING SUBTENDED BY A CHORD BEARING AND DISTANCE OF SOUTH 01°53'50" EAST, 17.00 FEET TO A POINT OF TANGENCY; THENCE SOUTH 03°32'22" WEST, 80.00 FEET TO A POINT OF CURVATURE OF A CURVE CONCAVE NORTHEASTERLY; THENCE SOUTHWESTERLY ALONG THE ARC OF SAID CURVE, HAVING A RADIUS OF 650.00 FEET AND A CENTRAL ANGLE OF 0°52'00", 226.90 FEET AND BEING SUBTENDED BY A CHORD BEARING AND DISTANCE OF SOUTH 33°02'26" WEST, 214.93 FEET TO A POINT OF TANGENCY; THENCE SOUTH 65°32'30" WEST, 135.37 FEET TO A POINT ON THE NORTHERLY LINE OF SELVA MARINA UNIT 2, ACCORDING TO THE PLAT THEREOF AS RECORDED IN PLAT BOOK 47, PAGES 85, 85A AND 85B OF THE PUBLIC RECORDS OF DUVAL COUNTY, FLORIDA; THENCE SOUTH 89°11'21" WEST ALONG SAID NORTHERLY LINE, 2.04 FEET TO THE NORTHWEST CORNER OF SAID PLAT AND A POINT ON THE EASTERLY LINE OF DONNER'S REPLAT, ACCORDING TO THE PLAT THEREOF AS RECORDED IN PLAT BOOK 19, PAGES 16 AND 16A OF SAID PUBLIC RECORDS; THENCE NORTH 73°00'05" WEST, 4.00 FEET TO THE SOUTHEAST CORNER OF SAID LOT 5, 175.96 FEET TO THE SOUTHWEST CORNER OF SAID LOT 5; THENCE NORTH 03°32'35" WEST ALONG THE WEST LINE OF SAID LOT 5, 70.96 FEET TO THE NORTHWEST CORNER OF SAID LOT 5, SAID POINT ALSO BEING ON THE SOUTH LINE OF THE AFOREMENTIONED SECTION 8; THENCE NORTH 89°07'49" EAST ALONG SAID SOUTH LINE OF SECTION 8, 3.89 FEET TO A POINT ON A CURVE CONCAVE SOUTHERLY; THENCE EASTERLY ALONG THE ARC OF SAID CURVE, HAVING A RADIUS OF 165.00 FEET AND A CENTRAL ANGLE OF 59°33'27", 171.51 FEET AND BEING SUBTENDED BY A CHORD BEARING AND DISTANCE OF NORTH 81°02'28" EAST, 163.89 FEET TO A POINT OF REVERSE CURVATURE OF A CURVE CONCAVE NORTHERLY; THENCE EASTERLY ALONG THE ARC OF SAID CURVE, HAVING A RADIUS OF 150.00 FEET AND A CENTRAL ANGLE OF 31°48'04", 83.25 FEET AND BEING SUBTENDED BY A CHORD BEARING AND DISTANCE OF SOUTH 85°05'50" EAST, 82.19 FEET; THENCE NORTH 03°32'22" EAST, 77.25 FEET; THENCE NORTH 109°23'38" WEST, 119.27 FEET TO A POINT OF CURVATURE OF A CURVE CONCAVE EASTERLY; THENCE NORTHERLY ALONG THE ARC OF SAID CURVE, HAVING A RADIUS OF 335.00 FEET AND A CENTRAL ANGLE OF 21°57'44", 128.41 FEET AND BEING SUBTENDED BY A CHORD BEARING AND DISTANCE OF NORTH 03°56'14" EAST, 127.62 FEET TO A POINT OF TANGENCY; THENCE NORTH 11°55'06" EAST, 88.85 FEET; THENCE NORTH 7°49'24" WEST, 45.00 FEET; THENCE NORTH 38°23'04" WEST, 534.60 FEET; THENCE NORTH 85°10'28" WEST, 57.45 FEET; THENCE NORTH 34°18'28" WEST, 128.87 FEET; THENCE NORTH 21°31'42" EAST, 77.21 FEET; THENCE NORTH 37°55'35" EAST, 63.03 FEET; THENCE NORTH 51°55'28" EAST, 80.74 FEET; THENCE NORTH 58°54'54" EAST, 37.77 FEET; THENCE NORTH 89°58'05" EAST, 149.49 FEET; THENCE SOUTH 28°40'49" EAST, 108.87 FEET; THENCE SOUTH 19°18'48" EAST, 95.34 FEET; THENCE SOUTH 38°23'04" EAST, 502.15 FEET TO A POINT OF CURVATURE OF A CURVE CONCAVE SOUTHWESTERLY; THENCE SOUTHEASTERLY ALONG THE ARC OF SAID CURVE, HAVING A RADIUS OF 320.00 FEET AND A CENTRAL ANGLE OF 33°17'49", 185.96 FEET AND BEING SUBTENDED BY A CHORD BEARING AND DISTANCE OF SOUTH 21°44'09" EAST, 183.36 FEET; THENCE SOUTH 56°04'58" EAST, 16.78 FEET; THENCE SOUTH 54°09'28" EAST, 163.83 FEET; THENCE NORTH 85°35'25" EAST, 66.34 FEET TO A POINT OF CURVATURE OF A CURVE CONCAVE NORTHEASTERLY; THENCE NORTHEASTERLY ALONG THE ARC OF SAID CURVE, HAVING A RADIUS OF 180.00 FEET AND A CENTRAL ANGLE OF 7°53'55", 24.81 FEET AND BEING SUBTENDED BY A CHORD BEARING AND DISTANCE OF NORTH 81°38'28" EAST, 24.79 FEET; THENCE SOUTH 14°27'25" EAST, 60.05 FEET; THENCE NORTH 75°32'35" EAST, 40.00 FEET; THENCE NORTH 14°27'25" WEST, 194.92 FEET; THENCE NORTH 75°32'35" EAST, 120.00 FEET; THENCE NORTH 14°27'25" WEST, 20.00 FEET; THENCE SOUTH 75°32'35" WEST, 120.00 FEET; THENCE NORTH 14°27'25" WEST, 37.76 FEET TO A POINT OF CURVATURE OF A CURVE CONCAVE SOUTHWESTERLY; THENCE NORTHWESTERLY ALONG THE ARC OF SAID CURVE, HAVING A RADIUS OF 150.00 FEET AND A CENTRAL ANGLE OF 18°13'51", 47.73 FEET AND BEING SUBTENDED BY A CHORD BEARING AND DISTANCE OF NORTH 23°34'20" WEST, 47.53 FEET TO A POINT OF TANGENCY; THENCE NORTH 32°41'16" WEST, 1333.06 FEET; THENCE NORTH 09°31'53" WEST, 178.01 FEET; THENCE NORTH 57°18'44" EAST, 30.00 FEET; THENCE NORTH 32°41'16" WEST, 20.00 FEET; THENCE NORTH 57°18'44" EAST, 20.00 FEET; THENCE NORTH 32°41'16" WEST, 55.93 FEET TO A POINT OF CURVATURE OF A CURVE CONCAVE NORTHEASTERLY; THENCE SOUTHEASTERLY ALONG THE ARC OF SAID CURVE, HAVING A RADIUS OF 200.00 FEET AND A CENTRAL ANGLE OF 23°09'23", 80.83 FEET AND BEING SUBTENDED BY A CHORD BEARING AND DISTANCE OF NORTH 21°08'34" WEST, 80.28 FEET TO A POINT OF TANGENCY; THENCE NORTH 93°15'53" WEST, 176.09 FEET TO A POINT OF CURVATURE OF A CURVE CONCAVE SOUTHWESTERLY; THENCE NORTHWESTERLY ALONG THE ARC OF SAID CURVE, HAVING A RADIUS OF 25.00 FEET AND A CENTRAL ANGLE OF 48°11'23", 21.03 FEET AND BEING SUBTENDED BY A CHORD BEARING AND DISTANCE OF NORTH 33°37'34" WEST, 20.41 FEET TO A POINT OF REVERSE CURVATURE OF A CURVE CONCAVE EASTERLY; THENCE NORTHERLY ALONG THE ARC OF SAID CURVE, HAVING A RADIUS OF 50.00 FEET AND A CENTRAL ANGLE OF 91°04'21", 78.48 FEET AND BEING SUBTENDED BY A CHORD BEARING AND DISTANCE OF NORTH 12°11'05" WEST, 71.37 FEET; THENCE NORTH 70°37'54" WEST, 40.35 FEET; THENCE NORTH 01°39'36" WEST, 130.26 FEET; THENCE NORTH 88°20'24" EAST, 103.38 FEET TO A POINT OF CURVATURE OF A CURVE CONCAVE SOUTHWESTERLY; THENCE SOUTHEASTERLY ALONG THE ARC OF SAID CURVE, HAVING A RADIUS OF 170.00 FEET AND A CENTRAL ANGLE OF 11°39'44", 337.04 FEET AND BEING SUBTENDED BY A CHORD BEARING AND DISTANCE OF SOUTH 34°51'44" EAST, 284.49 FEET; THENCE SOUTH 09°31'53" EAST, 178.14 FEET; THENCE SOUTH 20°11'06" EAST, 53.95 FEET; THENCE SOUTH 32°41'16" EAST, 1225.00 FEET; THENCE NORTH 54°09'28" EAST, 193.70 TO A POINT OF CURVATURE OF A CURVE CONCAVE SOUTHWESTERLY; THENCE SOUTHEASTERLY ALONG THE ARC OF SAID CURVE, HAVING A RADIUS OF 183.00 FEET AND A CENTRAL ANGLE OF 89°24'58", 254.62 FEET AND BEING SUBTENDED BY A CHORD BEARING AND DISTANCE OF SOUTH 81°38'04" EAST, 230.10 FEET TO A POINT OF COMPOUND CURVATURE OF A CURVE CONCAVE NORTHEASTERLY; THENCE SOUTHWESTERLY ALONG THE ARC OF SAID CURVE, HAVING A RADIUS OF 183.00 FEET AND A CENTRAL ANGLE OF 106°28'32", 340.08 FEET AND BEING SUBTENDED BY A CHORD BEARING AND DISTANCE OF SOUTH 15°48'39" WEST, 293.21 FEET TO A POINT OF TANGENCY; THENCE SOUTH 89°02'55" WEST, 78.97 FEET; THENCE SOUTH 63°20'12" WEST, 72.83 FEET TO A POINT ON A CURVE CONCAVE SOUTHWESTERLY; THENCE SOUTHEASTERLY ALONG THE ARC OF SAID CURVE, HAVING A RADIUS OF 440.00 FEET AND A CENTRAL ANGLE OF 12°12'23", 93.74 FEET AND BEING SUBTENDED BY A CHORD BEARING AND DISTANCE OF SOUTH 20°33'37" EAST, 93.56 FEET TO A POINT OF TANGENCY; THENCE SOUTH 14°27'25" EAST, 1.22 FEET; THENCE SOUTH 75°32'35" WEST, 120.00 FEET; THENCE SOUTH 14°27'25" EAST, 20.00 FEET; THENCE NORTH 75°32'35" EAST, 120.00 FEET; THENCE SOUTH 14°27'25" EAST, 569.00 FEET; THENCE SOUTH 75°32'35" WEST, 120.00 FEET; THENCE SOUTH 89°59'56" WEST, 51.63 FEET; THENCE SOUTH 75°32'35" WEST, 120.00 FEET; THENCE SOUTH 14°27'25" EAST, 282.19 FEET; THENCE SOUTH 101°7'57" EAST, 119.51 FEET; THENCE NORTH 79°42'03" EAST, 6.46 FEET; THENCE SOUTH 101°7'57" EAST, 25.00 FEET; THENCE SOUTH 24°33'36" EAST, 31.79 FEET; THENCE SOUTH 09°35'43" WEST, 138.57 FEET TO THE POINT OF BEGINNING.

SAID LANDS CONTAIN 40.3614 ACRES, MORE OR LESS

PREPARED BY:
RICHARD A. MILLER & ASSOCIATES, INC.
PROFESSIONAL LAND SURVEYORS
6701 BEACH BLVD., SUITE 6000
JACKSONVILLE, FLORIDA 32216
FAX (904) 721-5758
TELEPHONE (904) 721-1226

PSD NO.
CITY DEVELOPMENT NO. 0000.000

ADOPTION AND DEDICATION

This is to certify that ATLANTIC BEACH PARTNERS, LLC, a Florida Limited Liability Company, is the lawful owner of the lands described in the caption hereon known as ATLANTIC BEACH COUNTRY CLUB UNIT 2, having caused the same to be surveyed and subdivided. This plat being made in accordance with said survey is hereby adopted as a true and correct plat of those lands. All roads and unobstructed drainage easements, (except all private drainage easements which shall remain privately owned and the sole and exclusive property of ATLANTIC BEACH PARTNERS, LLC, its successors and assigns as shown hereon, and except all easements for utilities and sewers, which are hereby irrevocably dedicated and without reservation dedicated to JEA and the City of Atlantic Beach in accordance with the Interlocal Agreement Between the City of Jacksonville and the City of Atlantic Beach, Florida, dated July 31, 2013, are hereby irrevocably and without reservation dedicated to the City of Jacksonville, Florida, its successors and assigns and the City of Atlantic Beach, Florida, its successors and assigns in accordance with the Interlocal Agreement Between the City of Jacksonville and the City of Atlantic Beach, Florida, dated July 31, 2013. All water, sewer and re-use water facilities contained within public right of way are hereby irrevocably and without reservation dedicated to the City of Atlantic Beach. Tract "F" (Lift Station) is hereby dedicated to the City of Atlantic Beach.

The drainage easements hereby dedicated shall permit the City to discharge into said stormwater management facilities which these easements traverse, all water which may fall on or come upon the rights of way dedicated on this plat, together with all substances or matter which may flow or pass from said rights of way from adjacent land or from any other source of public waters into or through said stormwater management facilities, without any liability whatsoever on the part of the City for any damage, injuries or losses to persons or property resulting from the acceptance or use of these drainage easements by the City.

The stormwater management facilities shown on this plat are owned by Atlantic Beach Country Club Owners Association, Inc., its successors and assigns, and all maintenance and any other matters pertaining to said stormwater management facilities are the responsibility of Atlantic Beach Country Club Owners Association, Inc. The City by acceptance of this plat assumes no responsibility whatsoever for said stormwater management facilities.

The City shall not be liable nor responsible for the creation, operation, failure or destruction of water level control equipment which may be constructed or installed by the Owner or any other person within the area of the lands hereby platted, or of the stormwater management facilities shown on this plat, but shall have the right to maintain the water level in accordance with any state and local permits, including the repair, removal or replacement of the stormwater management facilities and the control structures to effect adequate drainage for the rights of ways dedicated hereon. Indemnify the City and save it harmless from Owner, its successors and assigns of the lands described and captioned hereon, shall forever release, discharge, indemnify the City and save it harmless from suits, action, damages, liability and expense in connection with loss of life, bodily or personal injury or property damage or any other damage arising from or out of any occurrence in, upon, at or from the stormwater management facilities described above, or any part thereof, occasioned wholly or in part by any act or omission of its agent, contractors, employees, servants, licensees or concessionaires within ATLANTIC BEACH COUNTRY CLUB UNIT 2. Owner's successors and assigns shall be subject to this release and indemnification and the covenants herein shall run with the land described and captioned hereon.

Those easements designated as "JEA-EE" are hereby irrevocably dedicated to JEA, its successors and assigns, for its exclusive use in conjunction with its underground electrical system. Those easements designated as "JEA-E" are hereby irrevocably dedicated to JEA, its successors and assigns, for its non-exclusive use in conjunction with its underground electrical system; provided however, that no parallel utilities may be installed within said easements.

Tract "E" (landscape), "G" (landscape), "H" (landscape), "I" (landscape), "J" (landscape), "K" (private road) and "L" (utilities) are hereby retained by the undersigned owner, its successors and/or assigns, provided however, the undersigned owner reserves the right to convey title to said tracts to an entity, including without limitation a property owners' association or other such entity as will assume all obligation of maintenance and operation thereof under the plat.

The 40 foot access, utility and drainage easements shown on Lots 112 through 115, 139 through 142, and 152 through 155, shall contain non-permanent improvements which would not impede use by City of Atlantic Beach. Any improvements located within the 40 foot access and drainage easements are subject to removal by City of Atlantic Beach for maintenance purpose(s) at the expense of the lot owner and/or Atlantic Beach Country Club Homeowner's Association.

In witness whereof, Atlantic Beach Partners, LLC, a Florida Limited Liability Company, has caused these presents to be executed this 10th day of November, 2014.

ATLANTIC BEACH PARTNERS, LLC
A Florida Limited Liability Company

By: The Wood Development Company of Jacksonville
Managing Member

James Ricky Wood, Jr.
James Ricky Wood, Jr. as President

Witness:

Jennifer Harris
(Print name)

Witness:

Katherine McDaniel
(Print name)

STATE OF FLORIDA
COUNTY OF DUVAL

The foregoing instrument was acknowledged before me this 10th day of November 2014 by James Ricky Wood as President of The Wood Development Company of Jacksonville as Managing Member of Atlantic Beach Partners, LLC, a Florida Limited Liability Company, on behalf of the company. He is personally known to me or has produced a driver's license as identification.

Notary Public State of Florida

Name: Katherine McDaniel

My Commission Expires: 3/12/15

My Commission Number is: EE015553

In witness whereof, the City of Jacksonville, a Florida Municipal Corporation, has caused these presents to be executed this 10th day of November, 2014.

COUNTRY CLUB FUNDING, LLC

This is to certify that pursuant to mortgage recorded in O.R.B. 16660, page 1269, the undersigned being the mortgagee of the lands described in the caption of this plat, does hereby join in and consent to the dedication of said lands and plat for the use and purpose therein described and agree that the mortgage shall be subordinated to said dedication.

WITNESS: Jennifer Harris
PRINT OR TYPE NAME

WITNESS: Katherine McDaniel
PRINT OR TYPE NAME

STATE OF FLORIDA
COUNTY OF DUVAL

The foregoing instrument was acknowledged before me this 10th day of November 2014 by Ashton Hudson as Authorized Representative of Country Club Funding, LLC. He is personally known to me or has produced a driver's license as identification.

Notary Public State of Florida

Name: Katherine McDaniel

My Commission Expires: 3/12/15

My Commission Number is: EE015553

TOLL BROS., INC.

This is to certify that pursuant to mortgage recorded in O.R.B. 16660, page 1321, the undersigned being the mortgagee of the lands described in the caption of this plat, does hereby join in and consent to the dedication of said lands and plat for the use and purpose therein described and agree that the mortgage shall be subordinated to said dedication.

WITNESS: Sandra Spencer
PRINT OR TYPE NAME

WITNESS: Marianne Wells
PRINT OR TYPE NAME

STATE OF FLORIDA
COUNTY OF DUVAL

The foregoing instrument was acknowledged before me this 12th day of November 2014 by Steve Merten as Designated Vice Pres. of Toll Bros., Inc., on behalf of the corporation. He is personally known to me or has produced a driver's license as identification.


Notary Public State of Florida

Name: Steve Merten

My Commission Expires: June 4, 2015

My Commission Number is: EE089096

PLAT BOOK 67 PAGE 132
SHEET 1 OF 6 SHEETS

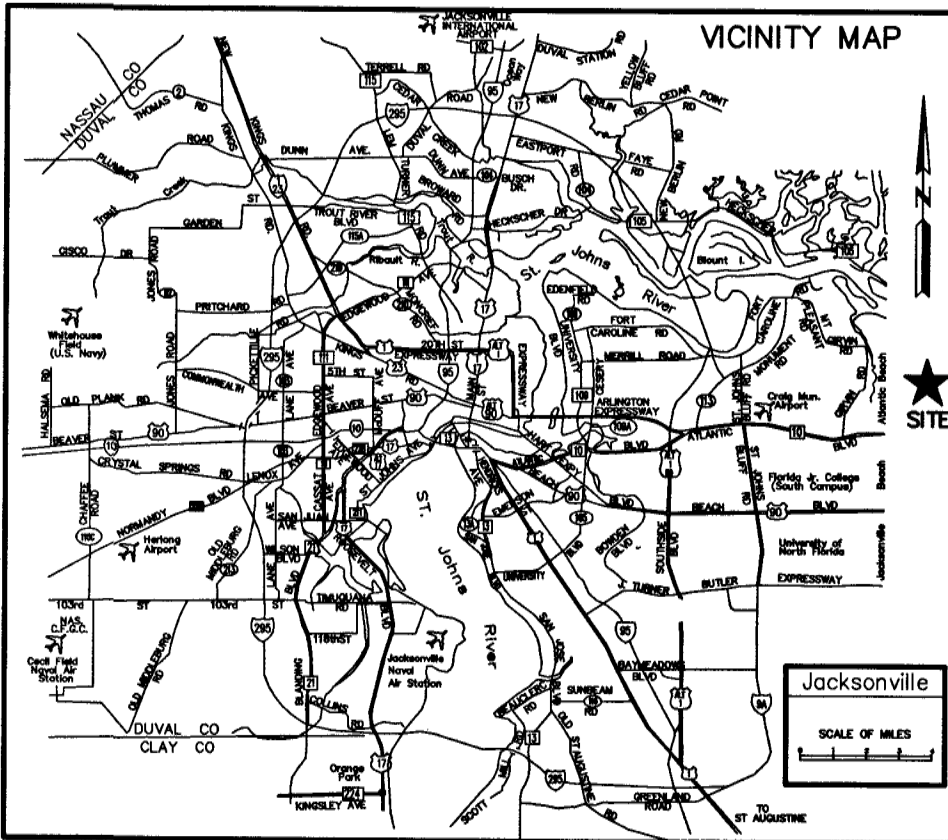

CITY OF ATLANTIC BEACH APPROVAL

This is to certify that this plat has been examined, accepted and approved by the City Commission of Atlantic Beach, Florida.

By: Mayor Carolyn Woods

Date: Nov 10, 2014

By: Donna L. Bartle

Date: Nov 10, 2014

APPROVED FOR THE RECORD

This is to certify that this plat has been examined, accepted and approved by the City of Jacksonville, Duval County, Florida, pursuant to Chapter 654, Ordinance Code.

By: James M. Robinson, Jr.

Director of Public Works

Date: 11/20/14

CLERK'S CERTIFICATE 2014 264374

This is to certify that this plat has been examined and approved by the City of Jacksonville, Duval County, Florida, and submitted to me for recording and is recorded in Plat Book 67, Page 132, of the current Public Records of Duval County, Florida, this 10th day of November 2014.

By: Ronne Fussen

Clerk of the Circuit Court

PLAT CONFORMITY REVIEW

This Plat has been reviewed and found in compliance with Part I, Chapter 177, Florida Statutes, this 20 day of November 2014.

By: William J. Merten

Professional Land Surveyor Number 3398

SURVEYOR'S CERTIFICATE

This is to certify that the above plat is a true and correct representation of the lands surveyed, platted and described above, that the survey was made under the undersigned's responsible direction and supervision, that the survey data complies with all of the requirements of the Florida Statute Chapter 177, that Permanent Reference Monuments, Permanent Control Points and lot corners have been monumented in accordance with Chapter 177.091 F. S., Chapter 5J-17 F. A. C. and Section 654.110 Ordinance Code of the City of Jacksonville.

Signed and Sealed this 10th day of November 2014.


By: William J. Merten

Florida Registered Land Surveyor
and Mapper Certificate No. 5843
L.B. No. 5189

ATLANTIC BEACH COUNTRY CLUB UNIT 2

Being a replat of all of Lot 5 of Donner's Replat and a portion Section 8 and Section 17, Township 2 South, Range 29 East, the City of Jacksonville, and the City of Atlantic Beach, Duval County, Florida

PLAT BOOK **67** PAGE **133**
SHEET 2 OF 6 SHEETS

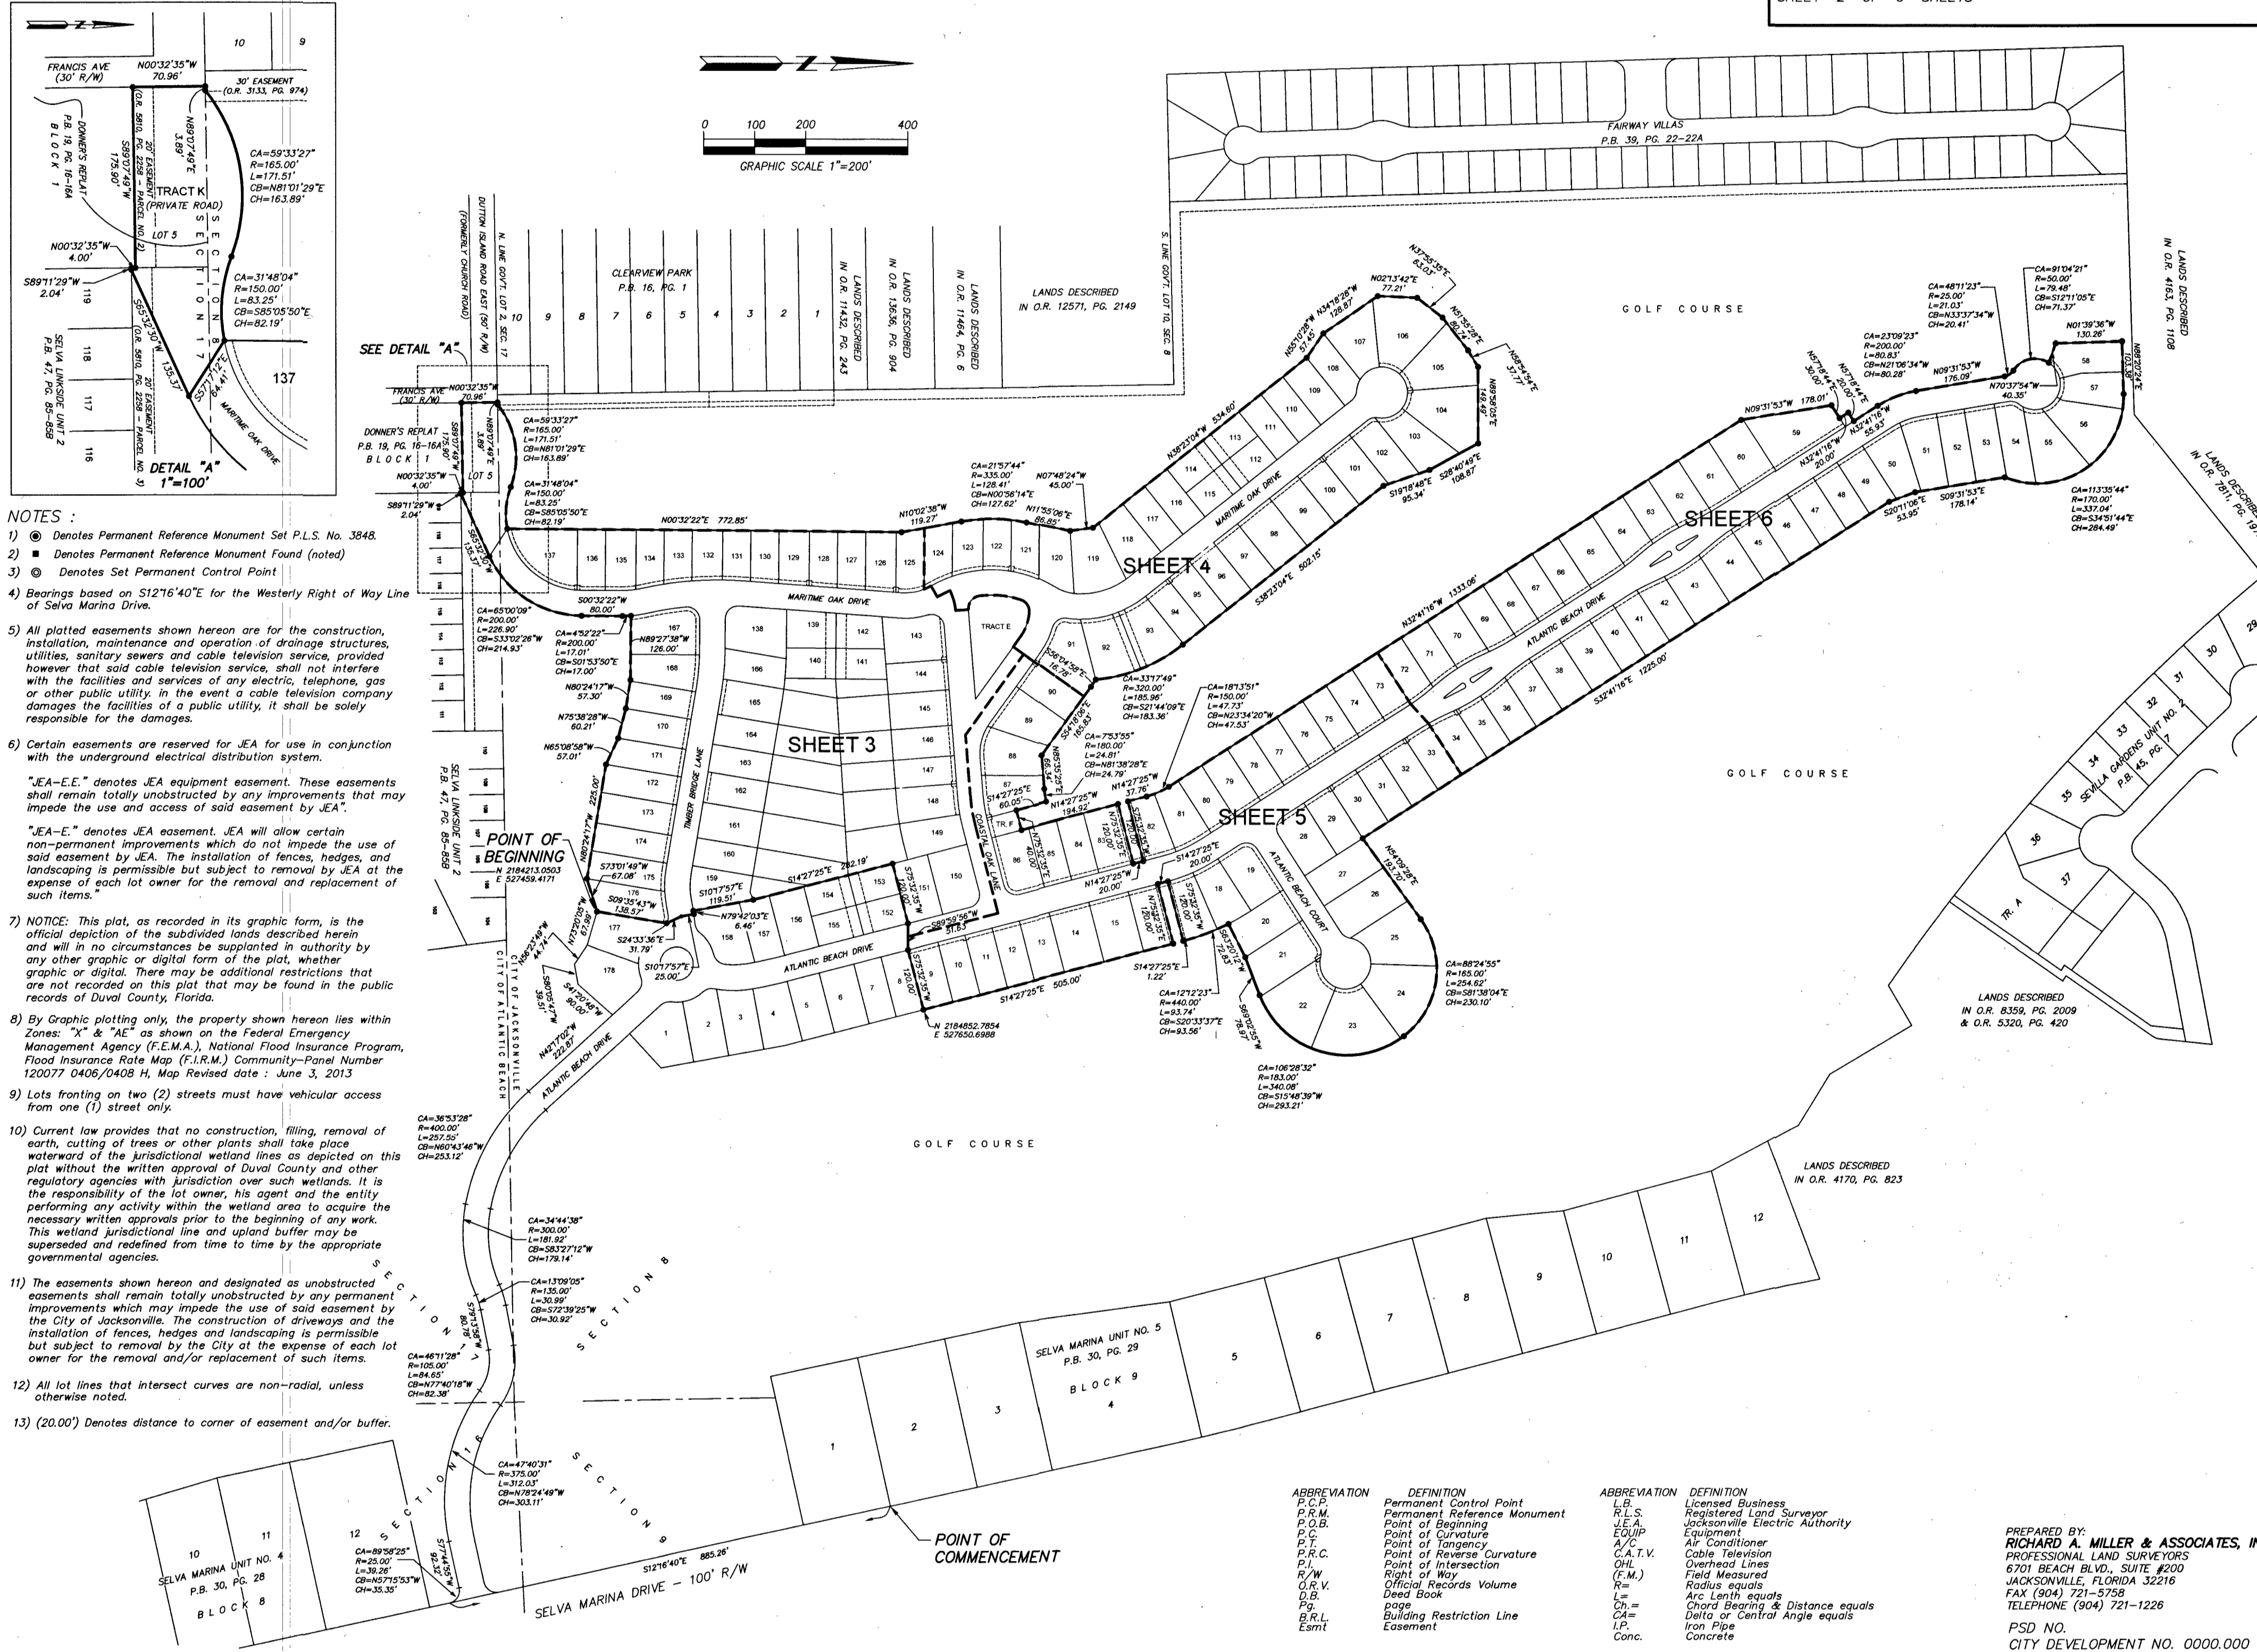

- NOTES:
- 1) $\odot$ Denotes Permanent Reference Monument Set P.L.S. No. 3848.
 - 2) $\blacksquare$ Denotes Permanent Reference Monument Found (noted).
 - 3) $\odot$ Denotes Set Permanent Control Point.
 - 4) Bearings based on S12°16'40"E for the Westerly Right of Way Line of Selva Marina Drive.
 - 5) All platted easements shown hereon are for the construction, installation, maintenance and operation of drainage structures, utilities, sanitary sewers and cable television service, provided however that said cable television service, shall not interfere with the facilities and services of any electric, telephone, gas or other public utility in the event a cable television company damages the facilities of a public utility, it shall be solely responsible for the damages.
 - 6) Certain easements are reserved for JEA for use in conjunction with the underground electrical distribution system.
"JEA-E.E." denotes JEA equipment easement. These easements shall remain totally unobstructed by any improvements that may impede the use and access of said easement by JEA.
"JEA-E." denotes JEA easement. JEA will allow certain non-permanent improvements which do not impede the use of said easement by JEA. The installation of fences, hedges, and landscaping is permissible but subject to removal by JEA at the expense of each lot owner for the removal and replacement of such items.
 - 7) NOTICE: This plat, as recorded in its graphic form, is the official depiction of the subdivided lands described herein and will in no circumstances be supplanted in authority by any other graphic or digital form of the plat, whether graphic or digital. There may be additional restrictions that are not recorded on this plat that may be found in the public records of Duval County, Florida.
 - 8) By Graphic plotting only, the property shown hereon lies within Zones: "X" & "AE" as shown on the Federal Emergency Management Agency (F.E.M.A.), National Flood Insurance Program, Flood Insurance Rate Map (F.I.R.M.) Community-Panel Number 120077 0406/0408 H, Map Revised date: June 3, 2013.
 - 9) Lots fronting on two (2) streets must have vehicular access from one (1) street only.
 - 10) Current law provides that no construction, filling, removal of earth, cutting of trees or other plants shall take place seaward of the jurisdictional wetland lines as depicted on this plat without the written approval of Duval County and other regulatory agencies with jurisdiction over such wetlands. It is the responsibility of the lot owner, his agent and the entity performing any activity within the wetland area to acquire the necessary written approvals prior to the beginning of any work. This wetland jurisdictional line and upland buffer may be superseded and redefined from time to time by the appropriate governmental agencies.
 - 11) The easements shown hereon and designated as unobstructed easements shall remain totally unobstructed by any permanent improvements which may impede the use of said easement by the City of Jacksonville. The construction of driveways and the installation of fences, hedges and landscaping is permissible but subject to removal by the City at the expense of each lot owner for the removal and/or replacement of such items.
 - 12) All lot lines that intersect curves are non-radial, unless otherwise noted.
 - 13) (20.00') Denotes distance to corner of easement and/or buffer.

ABBREVIATION	DEFINITION	ABBREVIATION	DEFINITION
P.C.P.	Permanent Control Point	L.B.	Licensed Business
P.R.M.	Permanent Reference Monument	R.L.S.	Registered Land Surveyor
P.O.B.	Point of Beginning	J.E.A.	Jacksonville Electric Authority
P.C.	Point of Curvature	EQUIP	Equipment
P.T.	Point of Tangency	A/C	Air Conditioner
P.R.C.	Point of Reverse Curvature	C.A.T.V.	Cable Television
E.I.	Point of Intersection	Q.U.L.	Overhead Lines
R/W	Right of Way	(F.M.)	Field Measured
O.R.V.	Official Records Volume	R=	Radius equals
D.B.	Deed Book	L=	Arc Length equals
Pg.	Page	Ch=	Chord Bearing & Distance equals
B.R.L.	Building Restriction Line	Ch=	Delta or Central Angle equals
Esmt	Easement	I.P.	Iron Pipe
		Conc.	Concrete

PREPARED BY:
RICHARD A. MILLER & ASSOCIATES, INC.
PROFESSIONAL LAND SURVEYORS
6701 BEACH BLVD., SUITE #200
JACKSONVILLE, FLORIDA 32216
FAX (904) 721-5758
TELEPHONE (904) 721-1226
PSD NO.
CITY DEVELOPMENT NO. 0000.000

ATLANTIC BEACH COUNTRY CLUB UNIT 2


Being a replat of all of Lot 5 of Donner's Replat and a portion of Section 8 and Section 17, Township 2 South, Range 29 East, the City of Jacksonville, and the City of Atlantic Beach, Duval County, Florida

PLAT BOOK 67 PAGE 134
SHEET 3 OF 6 SHEETS



PREPARED BY:
RICHARD A. MILLER & ASSOCIATES, INC.
PROFESSIONAL LAND SURVEYORS
6701 BEACH BLVD., SUITE #200
JACKSONVILLE, FLORIDA 32216
FAX (904) 721-5758
TELEPHONE (904) 721-1226

PSD NO.
CITY DEVELOPMENT NO. 0000.000

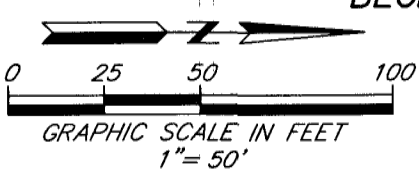


POINT OF BEGINNING

PLAT BOOK 67 PAGE 135

SHEET 4 OF 6 SHEETS


Being a replat of all of Lot 5 of Donner's Replat and a portion of Section 8 and Section 17, Township 2 South Range 29 East, the City of Jacksonville, and the City of Atlantic Beach, Duval County, Florida

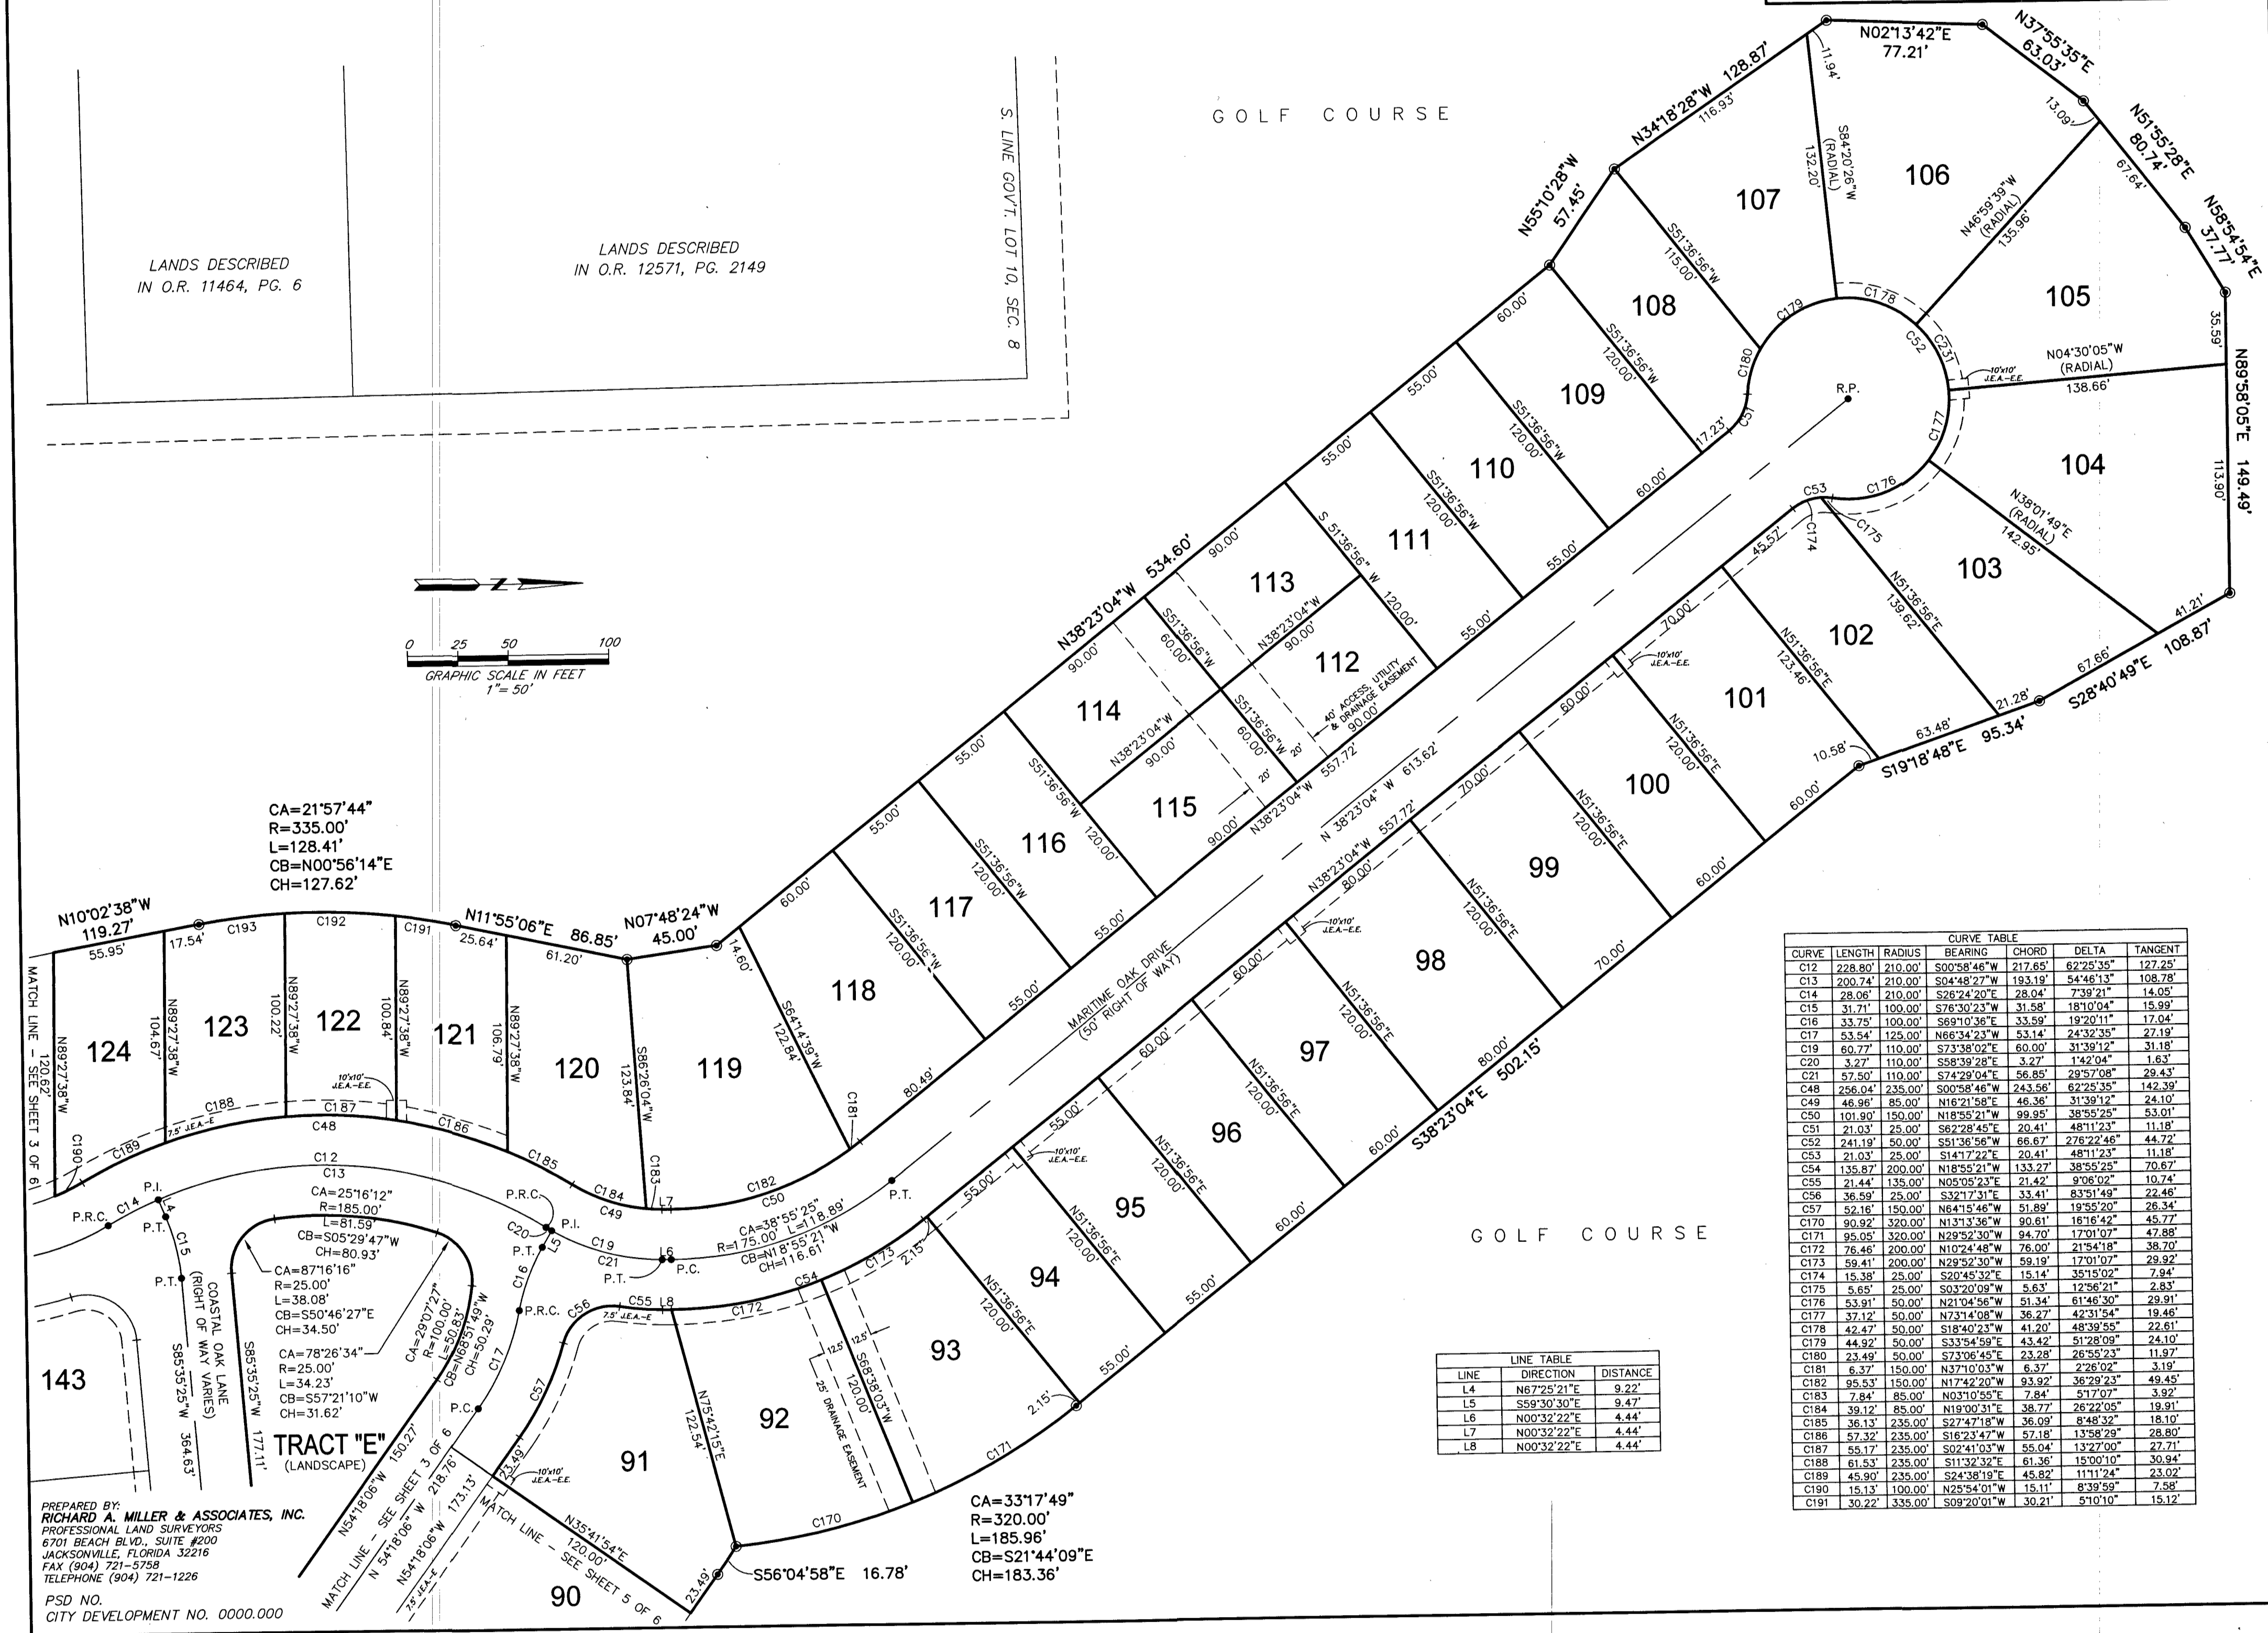

ATLANTIC BEACH COUNTRY CLUB UNIT 2

Being a replat of all of Lot 5 of Donner's Replat and a portion of Section 8 and Section 17, Township 2 South, Range 29 East, the City of Jacksonville, and the City of Atlantic Beach, Duval County, Florida

PLAT BOOK **67** PAGE **136**
SHEET 5 OF 6 SHEETS

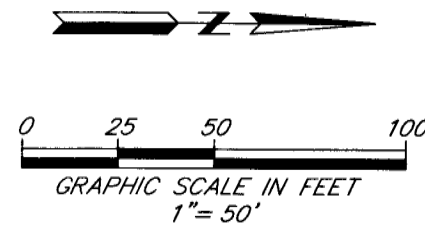

CURVE TABLE					
CURVE	LENGTH	RADIUS	BEARING	CHORD	DELTA
C18	56.99'	325.00'	N80°34'00"E	56.92'	10°02'50"
C58	70.00'	100.00'	S74°21'20"E	68.58'	40°06'29"
C59	52.61'	300.00'	S80°34'00"W	52.54'	10°02'50"
C60	39.27'	25.00'	S30°32'35"W	35.36'	90°00'00"
C61	85.91'	270.00'	N66°25'40"E	85.55'	18°13'51"
C62	63.31'	400.00'	N52°46'41"E	63.25'	9°04'27"
C78	63.31'	400.00'	S28°09'12"E	63.25'	9°04'07"
C79	39.27'	25.00'	N77°41'16"W	35.36'	90°00'00"
C80	21.03'	25.00'	S33°13'03"W	20.41'	48°11'23"
C81	24.18'	50.00'	N32°41'16"W	66.87'	27°22'46"
C82	21.03'	25.00'	S81°24'26"W	20.41'	48°11'23"
C83	39.27'	25.00'	N12°18'44"E	35.36'	90°00'00"
C84	101.82'	320.00'	N23°34'20"W	101.39'	18°13'51"
C108	50.50'	320.00'	N18°58'41"W	50.45'	9°02'32"
C109	51.32'	320.00'	N28°05'36"W	51.26'	9°11'19"
C110	69.44'	440.00'	N18°58'41"W	69.37'	9°02'32"
C111	70.56'	440.00'	N28°05'36"W	70.49'	9°11'19"
C112	46.26'	440.00'	N29°40'32"W	46.24'	6°01'28"
C113	1.28'	50.10'	S75°31'05"E	1.78'	2°02'24"
C114	71.07'	50.10'	N62°49'03"E	65.26'	81°17'19"

CA=18°13'51"
R=150.00'
L=47.73'
CB=N23°34'20"W
CH=47.53'

CA=7°53'55"
R=180.00'
L=24.81'
CB=N81°38'28"E
CH=24.79'

CURVE TABLE CONT'D					
CURVE	LENGTH	RADIUS	BEARING	CHORD	DELTA
C115	51.31'	50.10'	N07°10'07"W	49.10'	58°41'01"
C116	45.23'	50.00'	N62°26'14"W	43.72'	51°51'14"
C117	70.33'	50.00'	S51°20'32"W	64.67'	80°35'13"
C118	1.68'	50.00'	S10°05'08"W	1.68'	1°55'34"
C123	17.78'	400.00'	S31°24'51"E	17.78'	2°32'50"
C159	8.21'	400.00'	N33°20'51"W	9.21'	1°19'11"
C160	57.05'	270.00'	N26°38'04"W	56.95'	12°08'24"
C161	26.86'	270.00'	N17°31'08"W	26.84'	6°07'26"
C162	31.70'	150.00'	N26°38'04"W	31.64'	12°08'24"
C163	16.03'	150.00'	N17°31'08"W	16.02'	6°07'26"
C164	6.75'	300.00'	N76°11'15"E	6.75'	1°17'20"
C165	45.86'	300.00'	N81°12'40"E	45.81'	8°45'30"
C166	6.75'	180.00'	N76°37'03"E	6.75'	2°08'55"
C167	24.81'	180.00'	N81°38'28"E	24.79'	7°53'55"
C168	83.24'	100.00'	S73°17'34"E	62.19'	36°14'02"
C169	6.76'	100.00'	S56°14'20"E	6.76'	3°52'27"
C234	2.73'	183.00'	N68°37'15"E	2.73'	0°51'20"
C235	7.45'	183.00'	N36°15'41"W	7.44'	2°19'52"

CA=12°12'23"
R=440.00'
L=93.74'
CB=S20°33'37"E
CH=93.56'

CA=106°28'32"
R=183.00'
L=340.08'
CB=S15°48'39"W
CH=293.21'

CA=57°39'39"
R=183.00'
L=184.17'
CB=N06°15'56"W
CH=176.49'

CA=88°24'55"
R=165.00'
L=254.62'
CB=S81°38'04"E
CH=230.10'



PREPARED BY:
RICHARD A. MILLER & ASSOCIATES, INC.
PROFESSIONAL LAND SURVEYORS
6701 BEACH BLVD., SUITE #200
JACKSONVILLE, FLORIDA 32216
FAX (904) 721-5758
TELEPHONE (904) 721-1226
PSD NO.
CITY DEVELOPMENT NO. 0000.000

ATLANTIC BEACH COUNTRY CLUB UNIT 2

Being a replat of all of Lot 5 of Donner's Replat and a portion of Section 8 and Section 17, Township 2 South, Range 29 East, the City of Jacksonville, and the City of Atlantic Beach, Duval County, Florida

PLAT BOOK **67** PAGE **137**
SHEET 6 OF 6 SHEETS

CURVE	LENGTH	RADIUS	BEARING	CHORD	DELTA	TANGENT
C62	63.31'	400.00'	N52°46'41"E	63.25'	9°04'27"	31.72'
C63	126.62'	400.00'	N57°18'44"E	126.10'	18°08'15"	63.85'
C64	63.31'	400.00'	N61°50'48"E	63.25'	9°04'07"	31.72'
C65	63.31'	400.00'	S37°13'19"E	63.25'	9°04'07"	31.72'
C66	126.62'	400.00'	N32°41'16"W	126.10'	18°08'15"	63.85'
C67	63.31'	400.00'	N28°09'12"W	63.25'	9°04'07"	31.72'
C68	80.63'	200.00'	N21°06'34"W	80.28'	23°09'23"	40.97'
C69	21.03'	25.00'	N33°37'34"W	20.41'	48°11'23"	11.18'
C70	241.15'	50.00'	S80°28'07"W	68.67'	278°22'46"	44.72'
C71	21.03'	25.00'	S14°33'49"W	20.41'	48°11'23"	11.18'
C72	60.62'	150.00'	N21°06'34"W	60.21'	23°09'23"	30.73'
C73	63.31'	400.00'	N37°13'19"W	63.25'	9°04'07"	31.72'
C74	126.62'	400.00'	N32°41'16"W	126.10'	18°08'15"	63.85'
C75	63.31'	400.00'	S28°09'12"E	63.25'	9°04'07"	31.72'
C76	63.31'	400.00'	N37°13'19"W	63.25'	9°04'07"	31.72'
C77	126.62'	400.00'	N32°41'16"W	126.10'	18°08'15"	63.85'
C78	63.31'	400.00'	S28°09'12"E	63.25'	9°04'07"	31.72'
C124	45.55'	400.00'	S26°52'52"E	45.52'	6°31'27"	22.80'
C125	14.87'	400.00'	N24°41'04"W	14.87'	2°07'50"	7.44'
C126	55.12'	400.00'	N29°41'50"W	55.08'	7°53'43"	27.60'
C127	56.63'	400.00'	N37°13'19"W	56.38'	8°08'42"	28.36'
C128	3.88'	400.00'	S41°29'35"E	3.88'	0°31'36"	1.84'
C129	59.63'	400.00'	S36°57'31"E	59.58'	8°32'31"	29.87'
C130	22.79'	400.00'	S31°03'20"E	22.79'	3°15'51"	11.40'
C131	40.52'	400.00'	S26°31'16"E	40.51'	5°48'16"	20.28'
C132	19.91'	400.00'	N25°02'41"W	19.91'	2°51'06"	9.95'
C133	80.14'	400.00'	N32°12'36"W	80.00'	11°28'43"	40.20'
C134	26.58'	400.00'	N39°51'10"W	26.57'	3°48'26"	13.29'
C135	53.91'	400.00'	S37°53'46"E	53.87'	7°43'14"	27.00'
C136	9.41'	400.00'	S33°21'43"E	9.41'	1°20'53"	4.71'
C137	9.77'	50.00'	N33°03'30"E	9.76'	11°12'01"	4.90'
C138	37.60'	50.00'	N05°54'58"E	36.72'	43°05'02"	19.74'
C139	36.37'	50.00'	N37°36'38"W	37.44'	43°58'10"	20.19'
C140	37.98'	50.00'	N61°21'31"W	37.08'	43°31'36"	19.98'
C141	37.98'	50.00'	S55°06'53"W	37.08'	43°31'36"	19.98'
C142	79.48'	50.00'	N12°11'05"W	71.37'	91°04'21"	50.94'
C143	58.87'	170.00'	N10°34'53"E	58.57'	19°50'23"	29.73'
C144	113.14'	170.00'	N18°24'17"W	111.06'	38°07'56"	58.76'
C145	131.43'	170.00'	N59°37'08"W	128.18'	44°17'48"	69.20'
C146	22.99'	400.00'	N31°02'28"W	22.99'	3°17'35"	11.50'
C147	40.32'	400.00'	N26°30'25"W	40.30'	5°46'32"	20.18'
C148	30.16'	400.00'	S26°46'43"E	30.15'	4°19'10"	15.08'
C149	60.06'	400.00'	S32°14'23"E	60.00'	8°36'10"	30.09'
C150	36.41'	400.00'	S39°08'56"E	36.40'	5°12'55"	18.22'
C151	34.07'	400.00'	N39°18'58"W	34.06'	4°52'50"	17.05'
C152	29.24'	400.00'	N34°46'55"W	29.23'	4°11'18"	14.63'
C153	58.18'	400.00'	N28°31'15"W	58.15'	8°20'02"	29.14'
C154	5.13'	400.00'	N23°59'11"W	5.13'	0°44'05"	2.56'
C155	65.19'	400.00'	S28°17'17"E	65.12'	9°20'18"	32.67'
C156	60.25'	400.00'	S37°16'20"E	60.19'	8°37'48"	30.18'
C157	1.18'	400.00'	S41°40'19"E	1.18'	0°10'09"	0.59'
C158	54.10'	400.00'	N37°52'55"W	54.06'	7°44'56"	27.09'
C232	4.26'	170.00'	N21°13'06"E	4.26'	1°26'04"	2.13'
C233	29.35'	170.00'	N86°42'49"W	29.32'	9°53'34"	14.71'

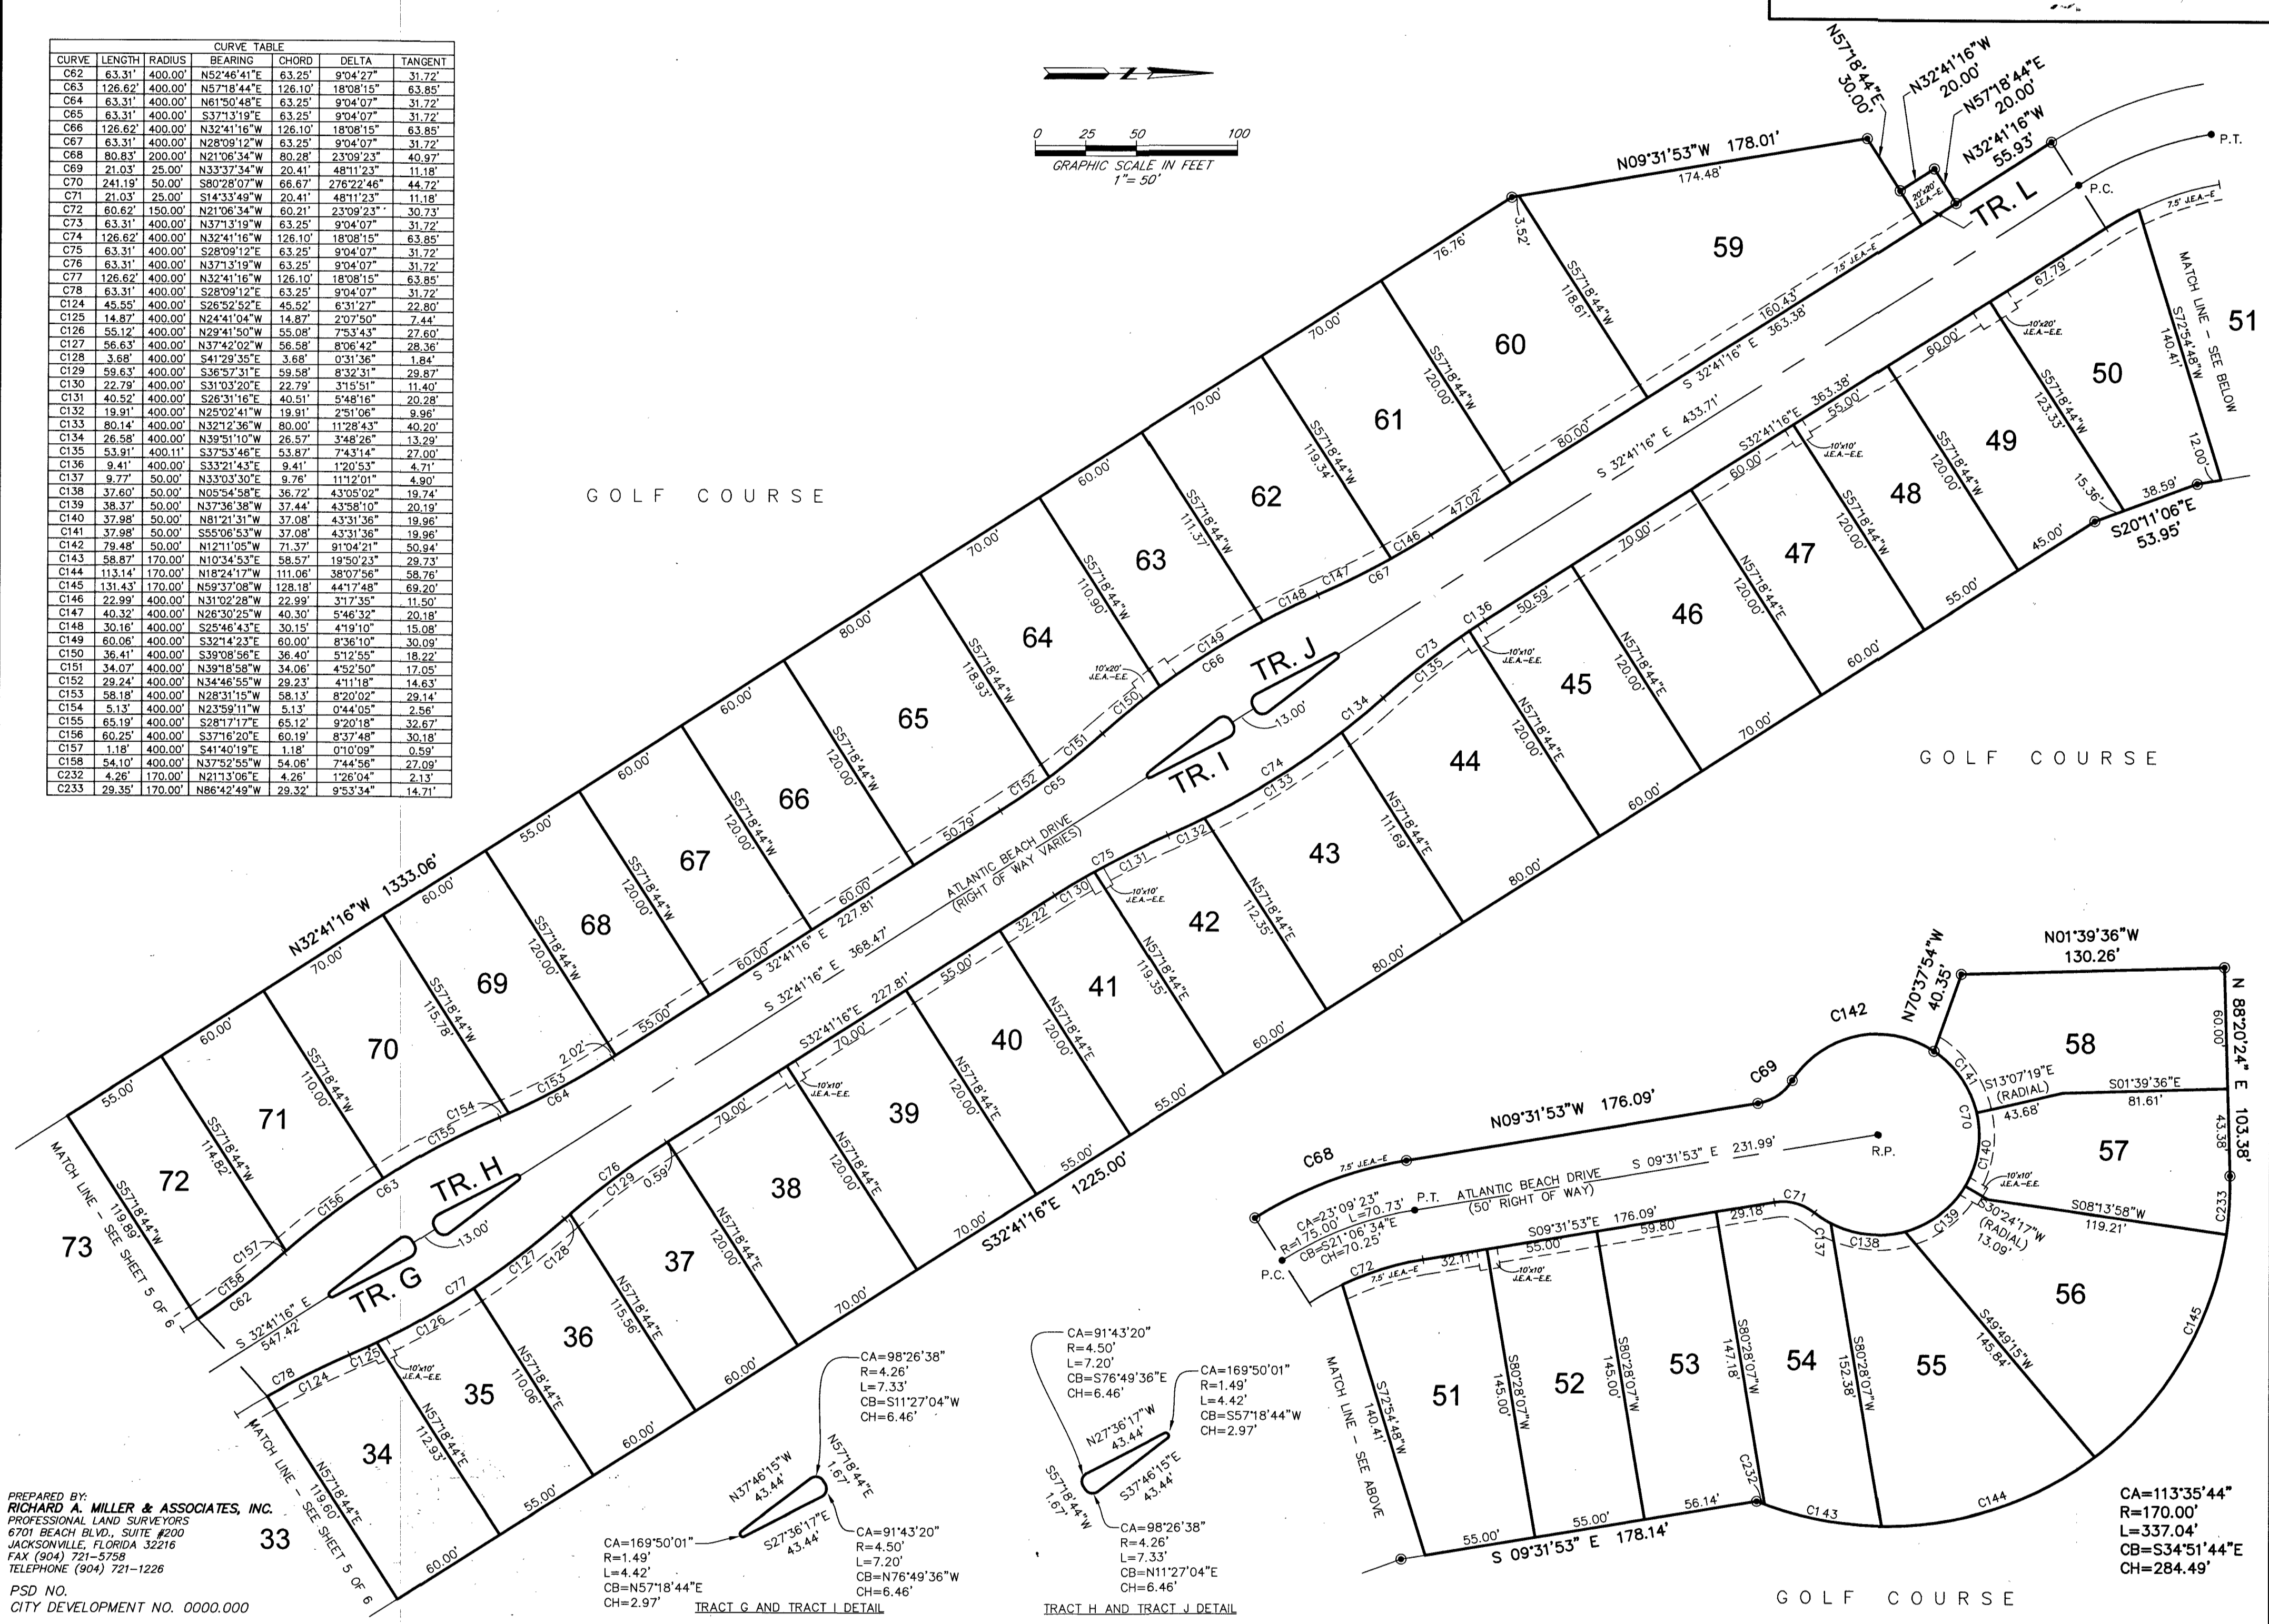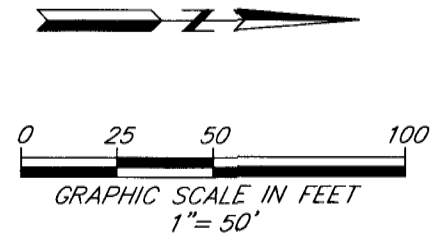

PREPARED BY:
RICHARD A. MILLER & ASSOCIATES, INC.
PROFESSIONAL LAND SURVEYORS
6701 BEACH BLVD., SUITE #200
JACKSONVILLE, FLORIDA 32216
FAX (904) 721-5758
TELEPHONE (904) 721-1226
PSD NO.
CITY DEVELOPMENT NO. 0000.000

CA=169°50'01"
R=1.49'
L=4.42'
CB=N57°18'44"E
CH=2.97'

CA=91°43'20"
R=4.50'
L=7.20'
CB=N76°49'36"W
CH=6.46'

CA=98°26'38"
R=4.26'
L=7.33'
CB=S76°49'36"E
CH=6.46'

CA=91°43'20"
R=4.50'
L=7.20'
CB=N76°49'36"W
CH=6.46'

CA=91°43'20"
R=4.50'
L=7.20'
CB=S76°49'36"E
CH=6.46'

CA=169°50'01"
R=1.49'
L=4.42'
CB=N76°49'36"W
CH=2.97'

CA=98°26'38"
R=4.26'
L=7.33'
CB=S76°49'36"E
CH=6.46'

CA=91°43'20"
R=4.50'
L=7.20'
CB=N76°49'36"W
CH=6.46'

CA=113°35'44"
R=170.00'
L=337.04'
CB=S34°51'44"E
CH=284.49'