

APPROVED
DATE 7-25-60
BY James H. Bell
COUNTY ENGINEER
James H. Bell
COUNTY ATTORNEY

BEACHWOOD UNIT TWO


BOOK 30 PAGE 82

Sheet One of Two Sheets

TAXES VERIFIED
- R & D

CAPTION:

Being a subdivision of a part of the Beachwood Acreage Replat recorded in Plat Book 29 Page 86 of the Current Public Records of Duval County, Florida, more particularly described as follows: commencing at the Northwest Corner of Section 32, Township 2 South, Range 28 East, thence run North 87°35'30" East 762.64 feet along the Northerly boundary line of said Section 32 to a point for the point of beginning, thence run South 2°24'30" East 130.50 feet; thence South 1°01'40" East 1509.24 feet; thence run North 89°18'20" East 50.00 feet; thence run South 1°01'40" East 100 feet; thence run North 89°18'20" East 377.53 feet to the Southwest corner of Lot 8, Block 10, Beachwood Unit One, a subdivision recorded in Plat Book 29, Pages 87 & 87A of the Current Public Records of Duval County, Florida; thence run North 0°41'40" West 100 feet; thence run North 3°24'42" East 60.16 feet; thence run North 0°41'40" West 200 feet; thence run North 27°15'10" West 67.09 feet; thence run North 0°41'40" West 102.20 feet; thence run North 75°27'25" West 120.71 feet; thence run North 35°18'20" East 120 feet; thence run North 4°16'43" West 77.88 feet; thence run North 35°18'20" East 100 feet; thence run North 39°04'03" East 60.14 feet; thence run North 35°18'20" East 62.53 feet; thence run North 35°18'20" East 140 feet; thence run South 54°41'40" East 300 feet; thence run North 35°18'20" East 100 feet; thence run North 39°04'03" East 60.14 feet; thence run North 35°18'20" East 260 feet; thence run South 54°41'40" East 100.16 feet; thence run along a curve to the left having a radius of 894.08 feet, a chord bearing South 57°53'59" East and a chord distance of 99.98 feet; thence run North 28°53'42" East 100 feet; thence run South 65°48'08" East 90.51 feet; thence run North 68°58'32" East 85.32 feet to the Northwest corner of Lot 4, Block 5 of said Beachwood Unit One; thence run North 0°41'40" West 1247.95 feet to the Northerly boundary line of said Section 32; thence run South 87°35'30" West 1626.37 feet along said Northerly boundary line to the point of beginning.

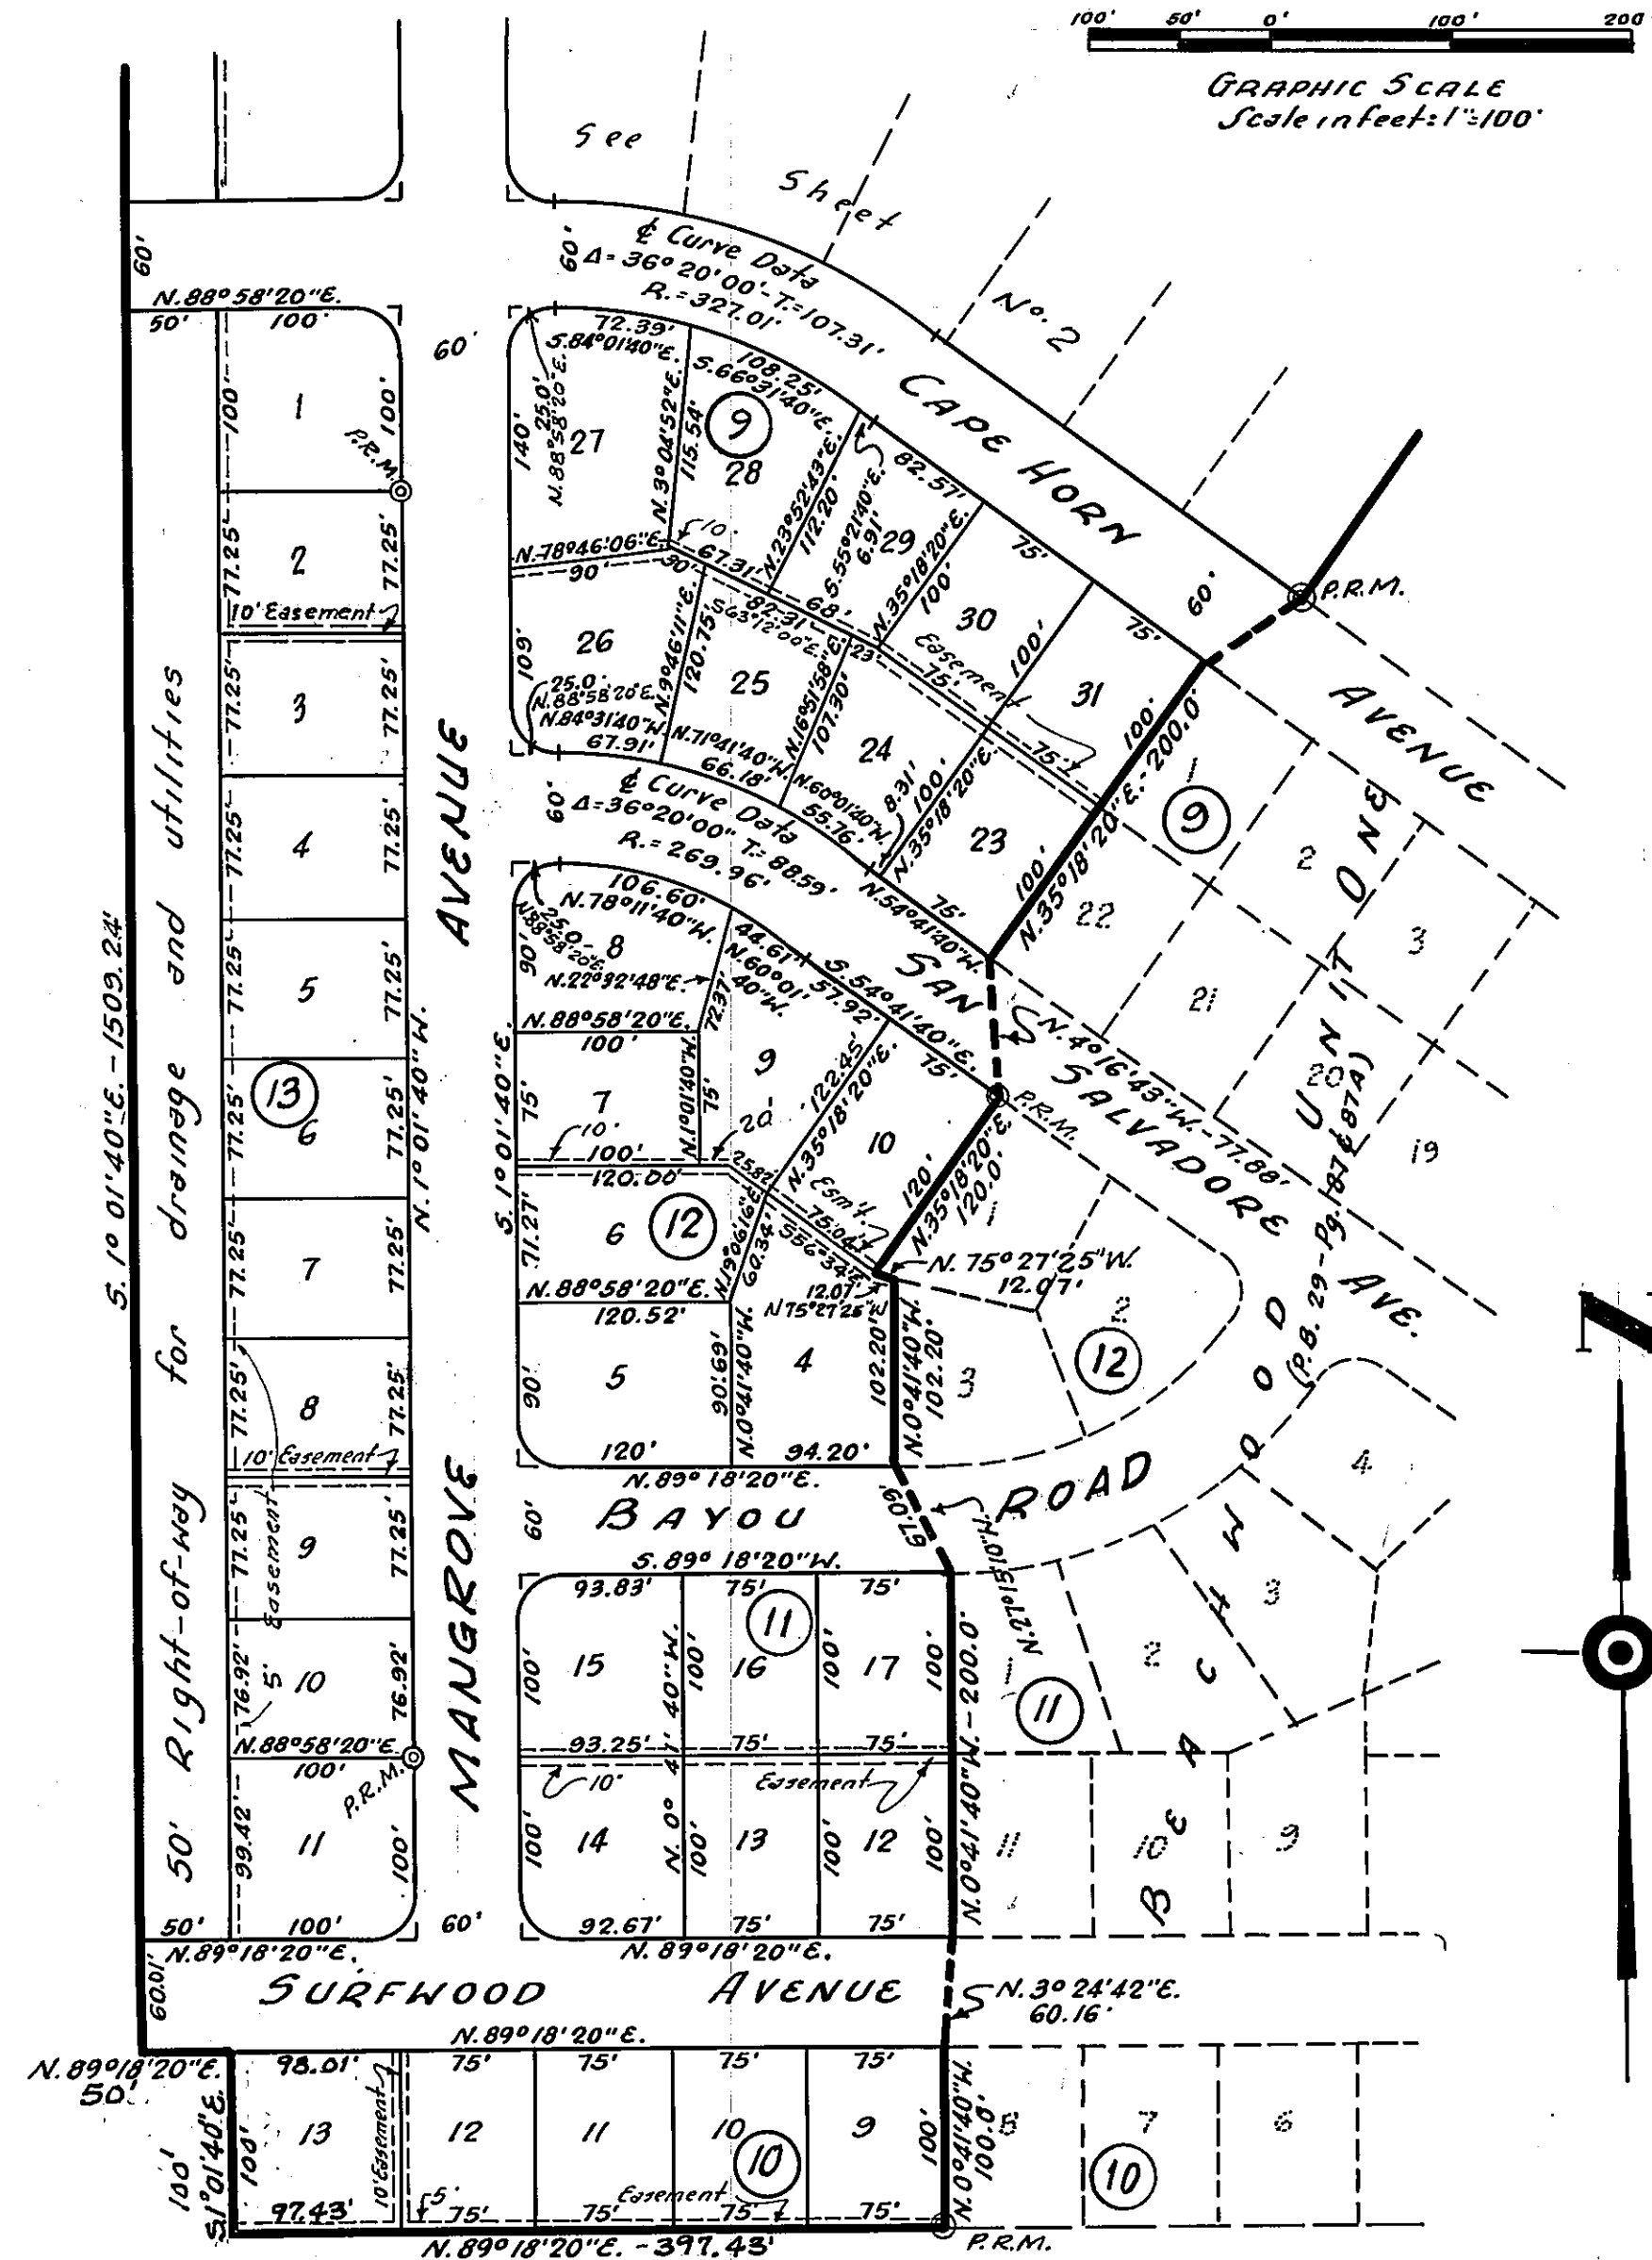

ADOPTION & DEDICATION

This is to certify that BEACH BOULEVARD ESTATES, INC., a corporation under the Laws of the State of Florida is the lawful owner of the lands described in the caption hereon and that it has caused the same to be surveyed and subdivided and this plat made in accordance with said survey is hereby adopted as the true and correct survey of said lands and all drives, avenues, boulevards, roads, easements and rights-of-way for drainage and utilities shown on said plat are hereby irrevocably and without reservations dedicated to the County of Duval and its successors.

In witness whereof BEACH BOULEVARD ESTATES, INC. has caused these presents to be signed by its President and Secretary respectively, by and with authority of its Board of Directors, in its name and with its corporate seal affixed this 1 day of JUNE A.D. 1960.
Signed and sealed
in the presence of:

Charles R. Bell Witness

M. A. Phil Witness

Alvin Sherman
President

Edward Lempka
Secretary

STATE OF FLORIDA COUNTY OF DUVAL

I hereby certify that on this day personally appeared before me, an officer duly authorized to administer oaths and take acknowledgements, Alvin Sherman and Edward Lempka respectively President and Secretary of BEACH BOULEVARD ESTATES, INC., a corporation under the Laws of the State of Florida to me well known to be the persons described in and who executed the foregoing dedication and who severally acknowledged before me that they executed the same freely and voluntarily as such officers for the uses and purposes therein expressed and that they affixed hereto the official seal of said corporation.

Witness my signature and official seal at Jacksonville, in the County of Duval and State of Florida this 1 day of JUNE A.D. 1960.

Thom Edward Lindberg
Notary Public State of Florida at large
My commission expires: 3-11-63

COMMISSIONER'S APPROVAL

Examined and approved this 25 day of JULY A.D. 1960 by the Board of County Commissioners of Duval County, Florida.

Leonard W. Thomas
Clerk

Tulbin Warren
Chairman

Percy M. Smith
Deputy Clerk

60- 57463

CLERK'S APPROVAL

I hereby certify that this plat has been examined and that it complies in form with Chapter No. 10275, Laws of Florida of 1925 and is filed for record and recorded in Plat Book 30 Pages 82 and 82A of the Public Records of Duval County, Florida this 16 day of Sept. A.D. 1960.

Leonard W. Thomas
Clerk

By Ellena
Deputy Clerk

SURVEYOR'S CERTIFICATE

This is to certify that the above plat is a correct representation of the lands surveyed and plotted and described above and that Permanent Reference Monuments have been placed according to the Laws of the State of Florida and that all the Duval County zoning rules and regulations have been complied with.

Signed this 31st day of May A.D. 1960.


"SIMMERSON, BELL & AKEL"

Charles R. Bell
Registered Surveyor Certificate No. 1337

BEACHWOOD UNIT TWO

BOOK 30 PAGE 82A

Sheet 2 of 2 Sheets

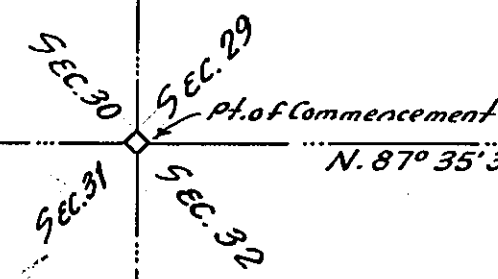

- "NOTES"**
1. Bearings and distances shown on curves are chord bearings and distances.
 2. Distances shown on block corners are to street line intersections.
 3. Building restriction and setback lines are 25 feet from street line.
 4. All radii not shown are 25 feet.
 5. Permanent Reference Monuments are shown thus: P.R.M.
 6. Easements are for drainage & utilities.
 7. Tract "A" is reserved for Sewage Lift Station.

