



# HICKS SUBDIVISION

OF THE N.W. 1/4 OF THE N.E. 1/4 OF  
SEC 12, T. 2 S., R. 25 E.


AS SURVEYED  
BY ELLIS, CURTIS & KOOKER  
JACKSONVILLE, FLA.  
SCALE 1"=100'  
MARCH 30, 1912

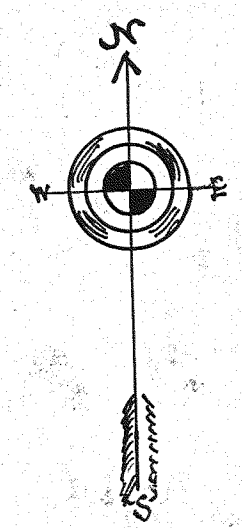

This is to certify that the above plat indicates  
and is made in accordance with an actual survey  
of the lands described in the above caption to  
said plat, as made by us.

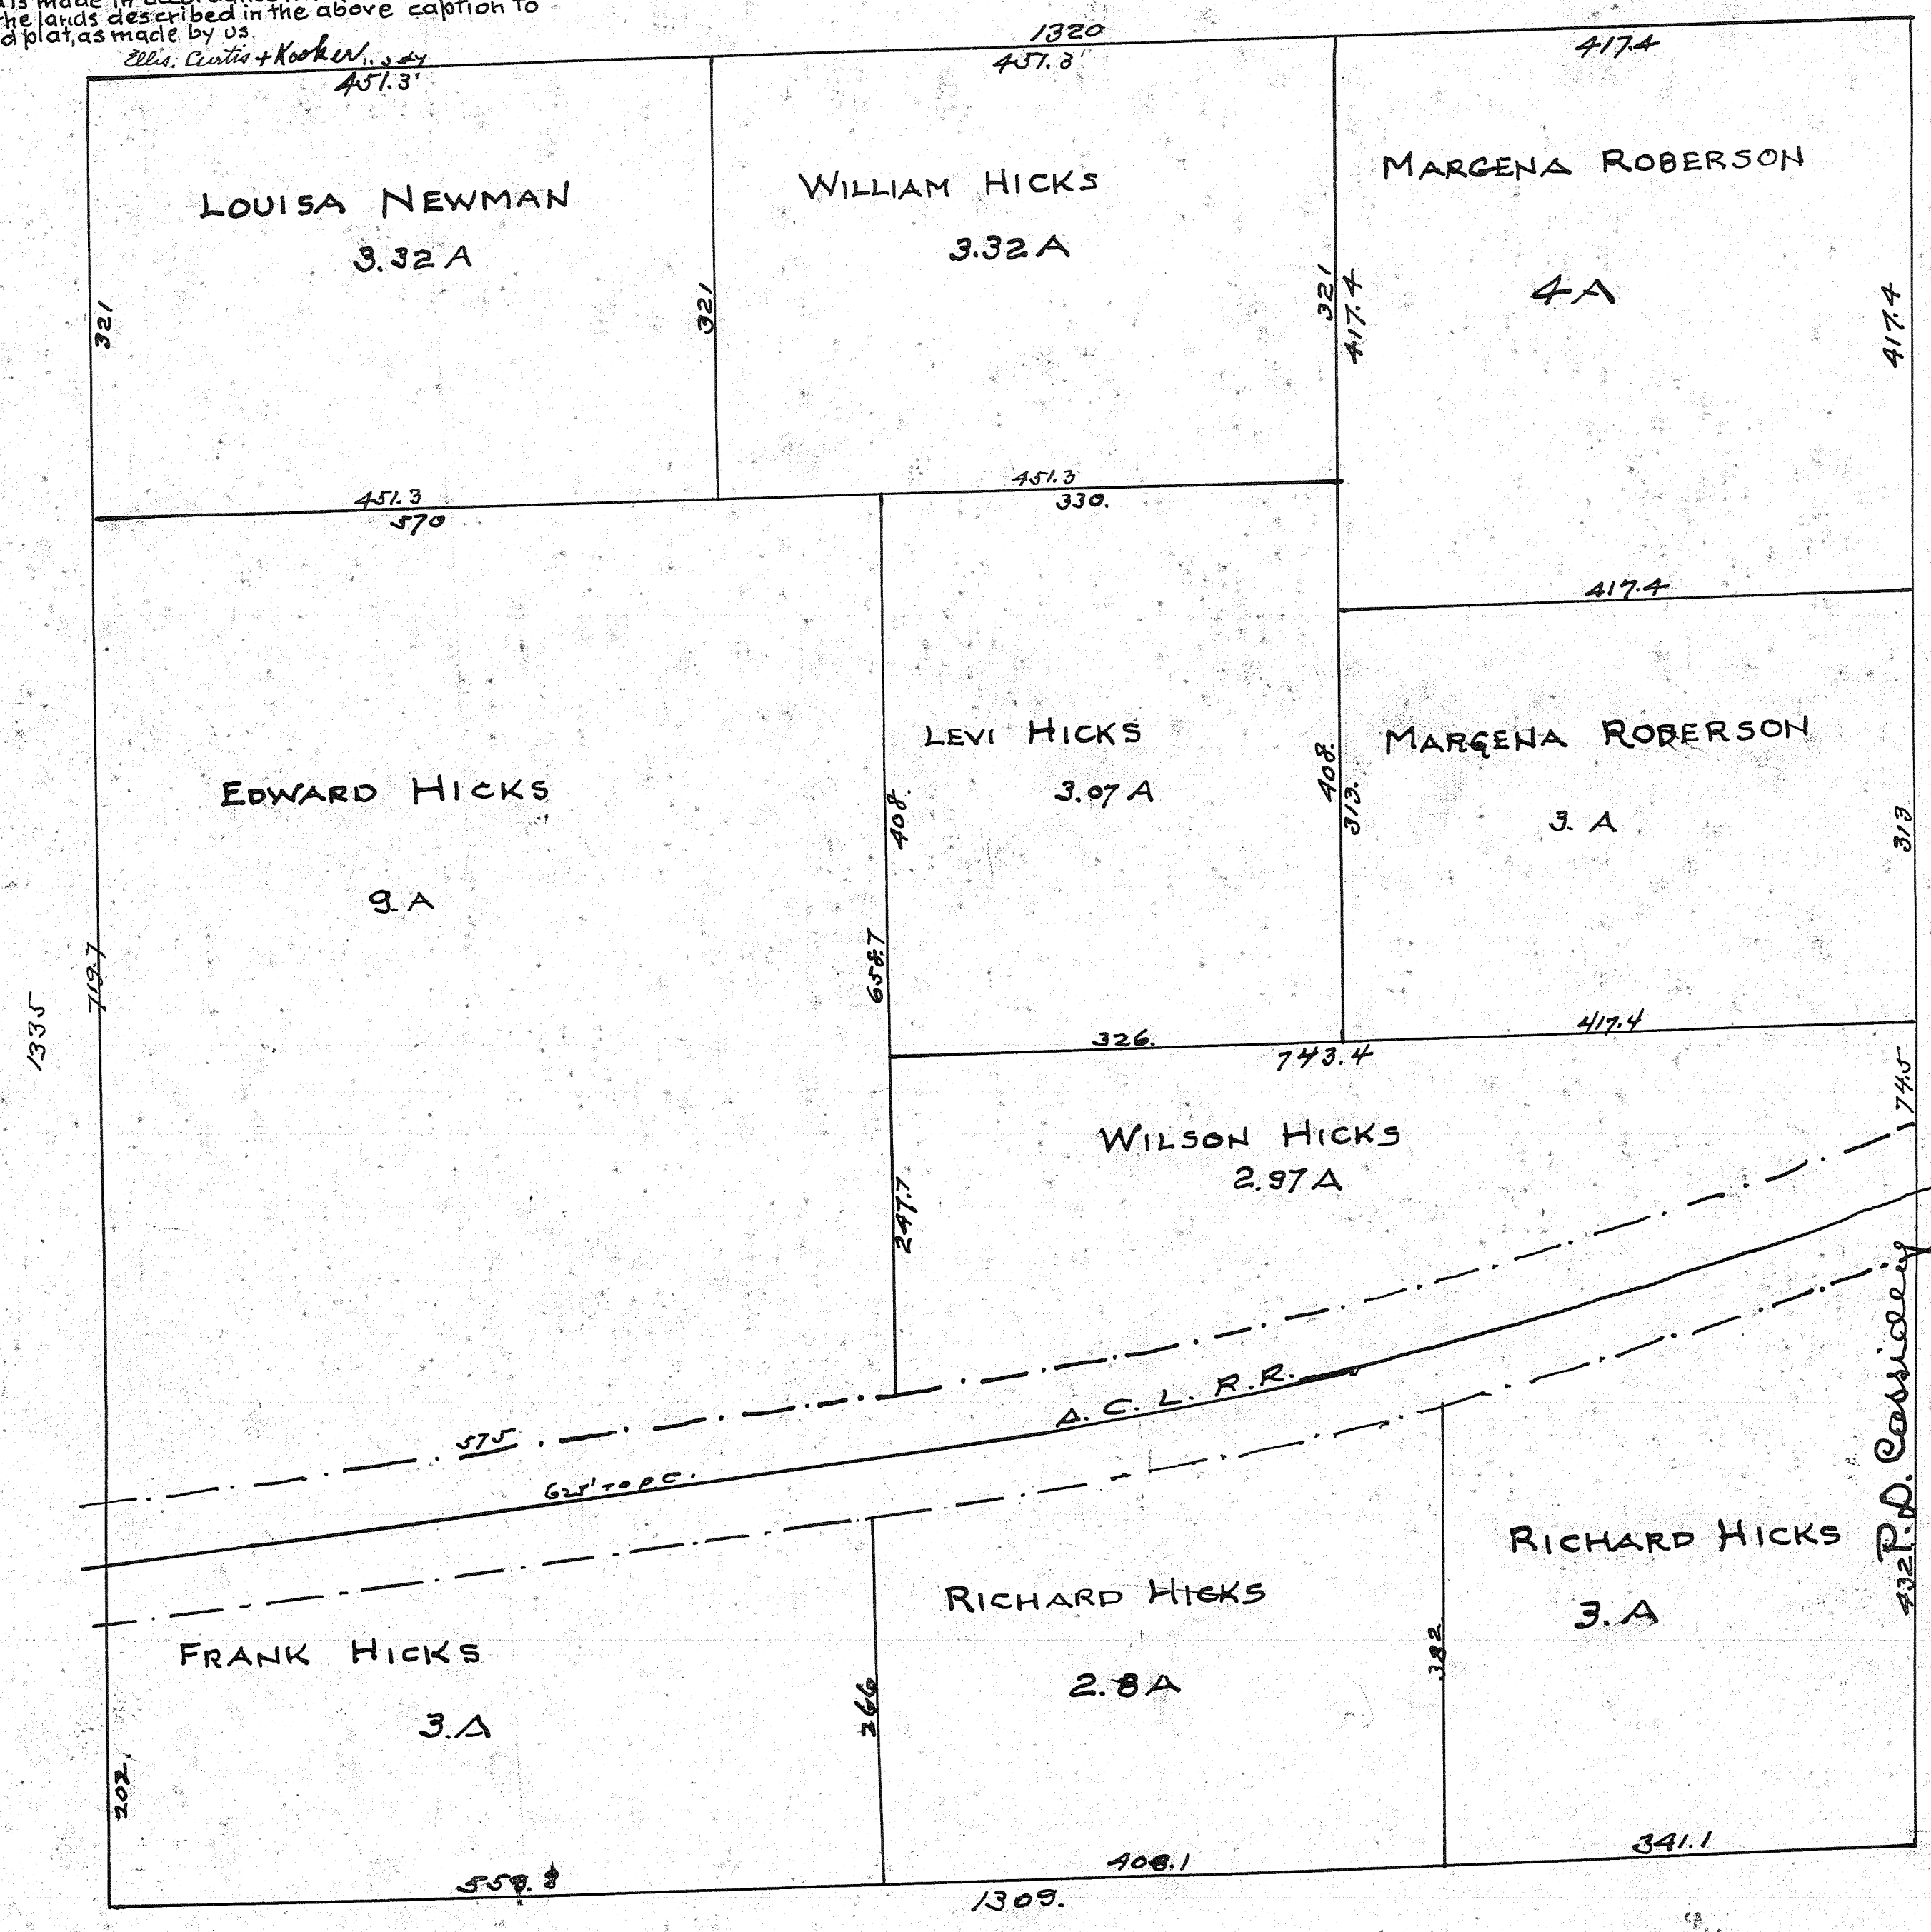

Filed and Recorded in the Public Records of Duval County Fla. this 19th day of April 1912, in Plat Book 124 folio 85. Record Verified.  
P. D. Cassidy, CLERK, BY

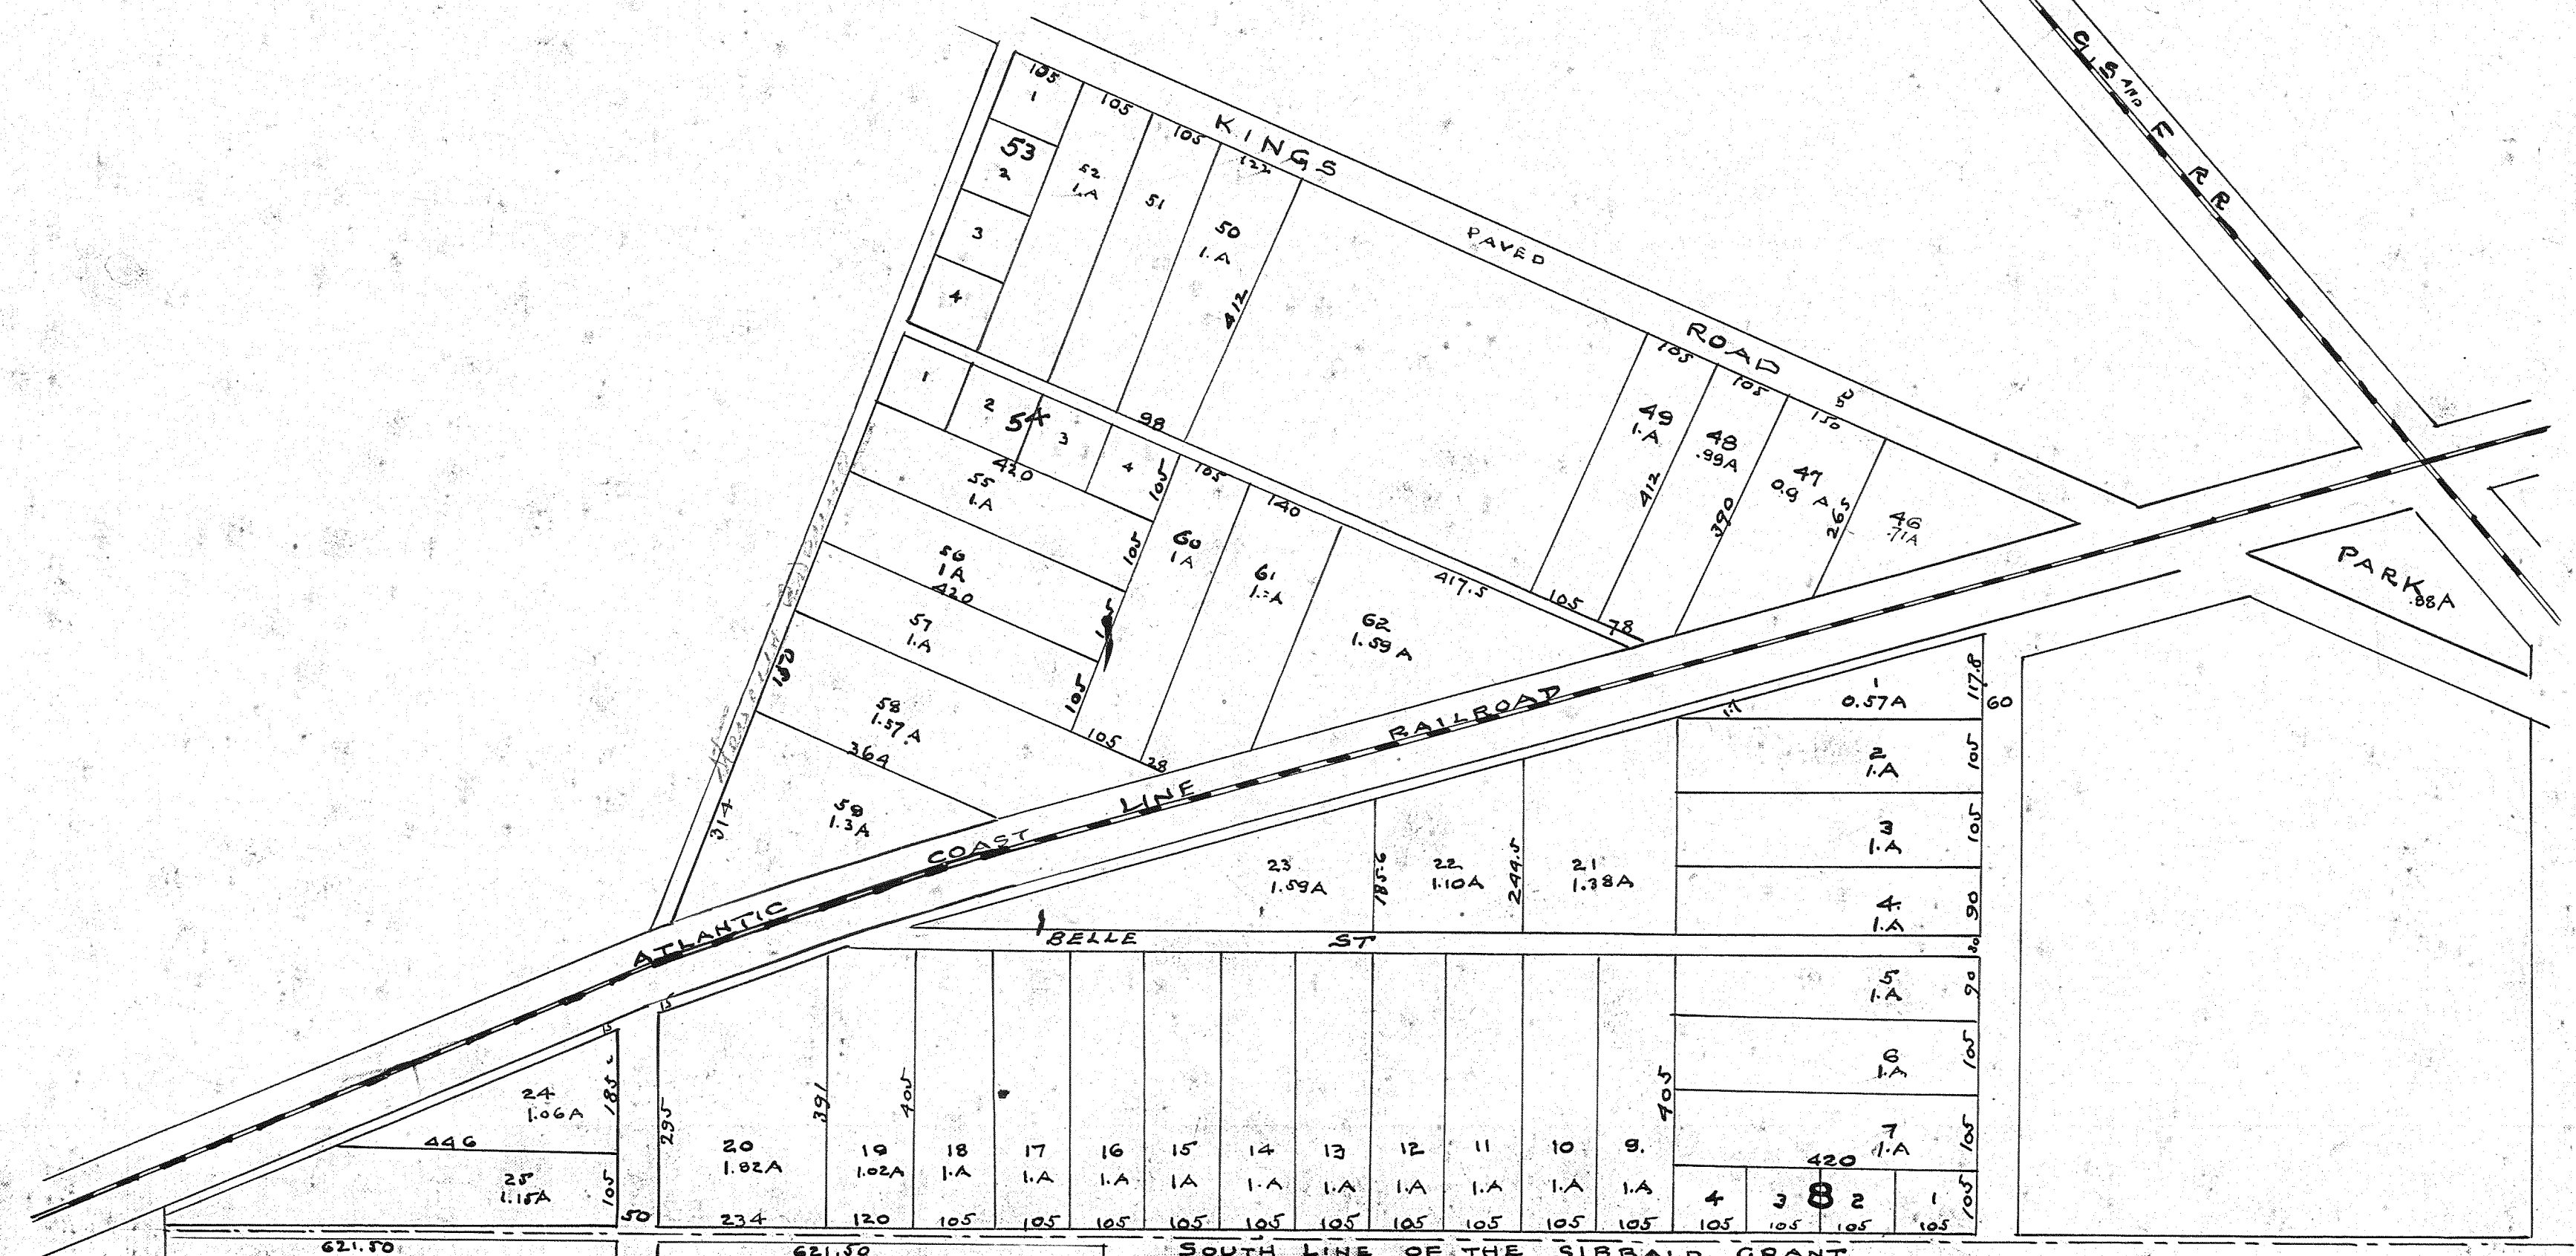

# JOHN M. STEVENS SUBDIVISION OF PART OF THE CHAS. F. SIBBALD GRANT SEC 55 NO. 4 SEC 5 T. 2 S., R. 26 E. DUVAL COUNTY FLORIDA

SURVEYED 1908 SCALE 1"=200'  
BY ELLIS, CURTIS & KOOKER  
CIVIL ENGINEERS & SURVEYORS  
JACKSONVILLE FLORIDA

This is to certify that the above plat, made as  
authorized, is hereby adopted as a true and correct  
plat of lands described in legend thereto.  
In witness whereof I have hereunto set my hand  
and seal this 17th day of December A.D. 1910.

Executed in the presence of us.

*J. D. Shaw*  
*Chas. F. Sibbald*

|    |        |    |        |
|----|--------|----|--------|
| 25 | 2.5 A  | 26 | 2.5 A  |
| 44 | 2.5 A  | 27 | 2.5 A  |
| 43 | 2.5 A  | 28 | 2.5 A  |
| 42 | 2.5 A  | 29 | 2.5 A  |
| 41 | 2.5 A  | 30 | 2.5 A  |
| 40 | 2.5 A  | 31 | 2.5 A  |
| 39 | 2.5 A  | 32 | 2.5 A  |
| 38 | 2.5 A  | 33 | 2.5 A  |
| 37 | 2.16 A | 34 | 2.16 A |
| 36 | 2.16 A | 35 | 2.16 A |

Filed & Recorded in the Public Records of Duval County Fla. this 19th day of April 1912, in Plat Book 4 folio 85.  
Record Verified.

P. D. Cassidy, CLERK.  
BY E. C. Clark, D.C.